



FOR APPROVAL - NOT FOR CONSTRUCTION

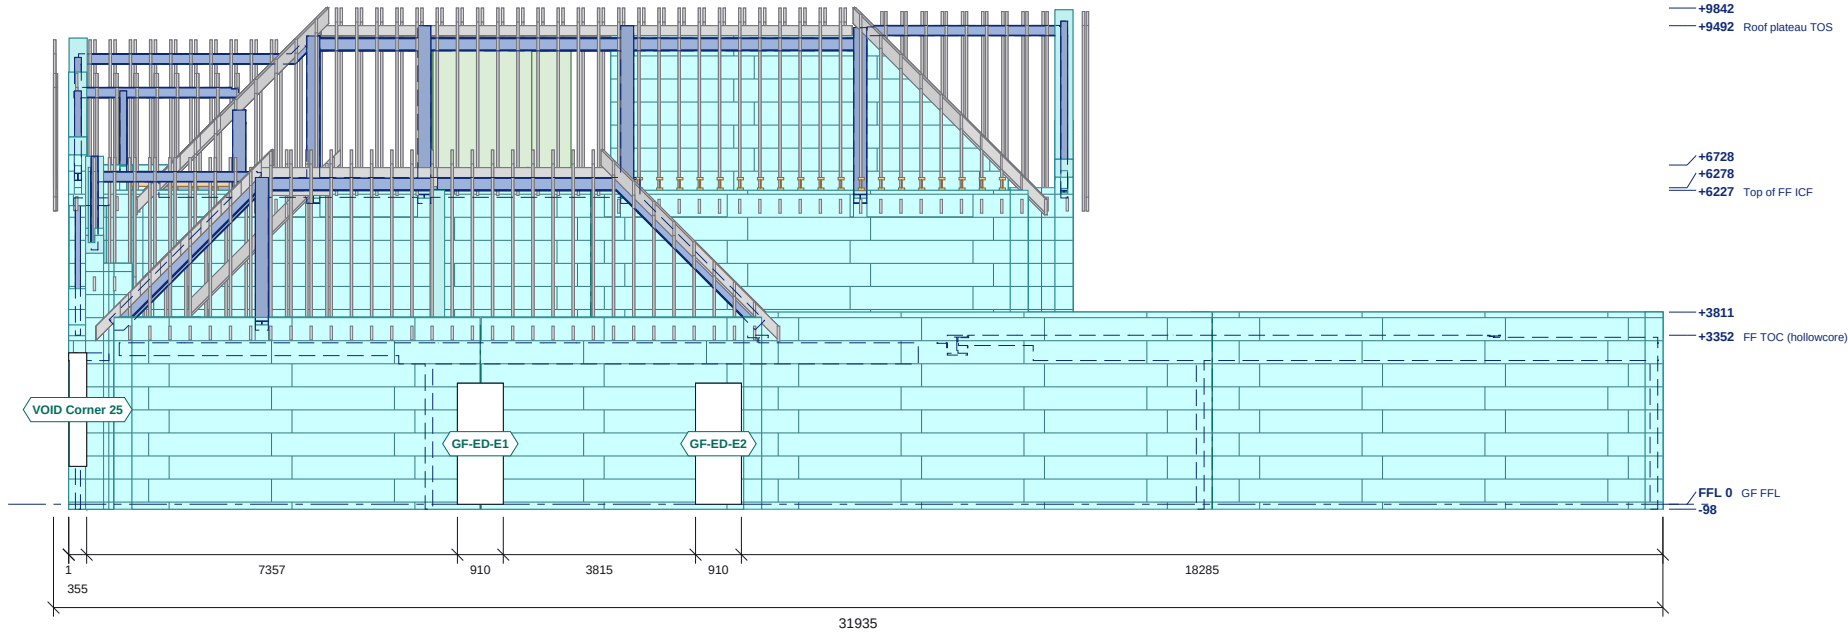

EAST ELEVATION

Scale 1:150 @ A3 | Levels above GF FFL (AOD in the schedule); sills and heads in the schedule

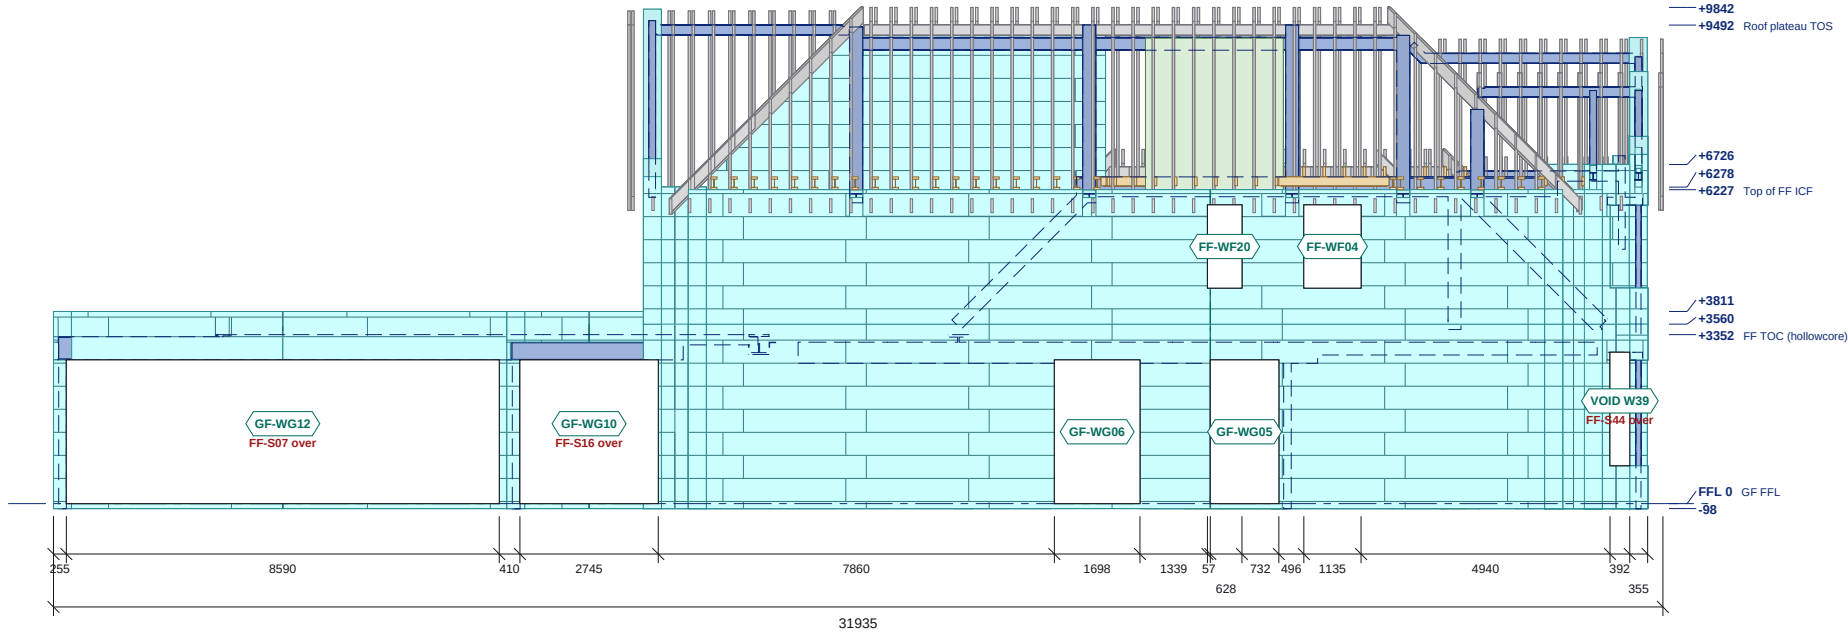

WEST ELEVATION

Scale 1:150 @ A3 | Levels above GF FFL (AOD in the schedule); sills and heads in the schedule



- ICF external EPS face
- Block course joint
- Stack joint
- Steel
- Roof build-up (slab / earth / sedum)

ELEVATION SCHEDULES

EAST ELEVATION: OPENINGS

| Ref            | Width | Height | Sill | Head  | Lintel |
|----------------|-------|--------|------|-------|--------|
| GF-ED-E1       | 910   | 2400   | 0    | +2400 | -      |
| GF-ED-E2       | 910   | 2400   | 0    | +2400 | -      |
| VOID Corner 25 | 356   | 2250   | +752 | +3002 | -      |

Structural openings in the ICF, sill and head above GF FFL.

WEST ELEVATION: OPENINGS

| Ref      | Width | Height | Sill  | Head  | Lintel      |
|----------|-------|--------|-------|-------|-------------|
| FF-WF04  | 1135  | 1650   | +4275 | +5925 | -           |
| FF-WF20  | 685   | 1650   | +4275 | +5925 | -           |
| GF-WG05  | 1360  | 2850   | 0     | +2850 | -           |
| GF-WG06  | 1698  | 2850   | 0     | +2850 | -           |
| GF-WG10  | 2745  | 2850   | 0     | +2850 | FF-S16 over |
| GF-WG12  | 8590  | 2850   | 0     | +2850 | FF-S07 over |
| VOID W39 | 392   | 2250   | +752  | +3002 | FF-S44 over |

Structural openings in the ICF, sill and head above GF FFL.

EAST ELEVATION: LEVELS

| Level                | FFL   | AOD     |
|----------------------|-------|---------|
| underside of ICF     | -98   | 168.650 |
| GF FFL               | 0     | 168.748 |
| FF TOC (hollowcore)  | +3352 | 172.100 |
| top of ICF           | +3811 | 172.559 |
| Top of FF ICF        | +6227 | 174.975 |
| top of ICF           | +6278 | 175.026 |
| top of ICF           | +6728 | 175.476 |
| Roof plateau TOS     | +9492 | 178.240 |
| top of roof build-up | +9842 | 178.590 |

WEST ELEVATION: LEVELS

| Level                | FFL   | AOD     |
|----------------------|-------|---------|
| underside of ICF     | -98   | 168.650 |
| GF FFL               | 0     | 168.748 |
| FF TOC (hollowcore)  | +3352 | 172.100 |
| top of ICF           | +3560 | 172.308 |
| top of ICF           | +3811 | 172.559 |
| Top of FF ICF        | +6227 | 174.975 |
| top of ICF           | +6278 | 175.026 |
| top of ICF           | +6726 | 175.474 |
| Roof plateau TOS     | +9492 | 178.240 |
| top of roof build-up | +9842 | 178.590 |

NOTES

- ICF: Nudura 6" XR35, 101.6 EPS + 152.4 core + 101.6 EPS = 355.6; 6" Std, 66.7 EPS + 152.4 core + 66.7 EPS = 285.8. External EPS face shown with the block course joints, vertical block joints and stack joints as populated.
- Levels above GF FFL (168.748 AOD). Openings are structural openings in the ICF; glazing, doors, render and finishes by others, not shown.
- Steel, roof build-up and masonry shown as modelled.
- See UKPCS-003-GA-01 for plan setting out, lintels and steel.

REVISIONS

| REV | DATE     | DESCRIPTION    |
|-----|----------|----------------|
| P01 | 23.09.26 | Approval issue |



|           |          |
|-----------|----------|
| CLIENT    | PROJECT  |
| ICF Homes | Dendrons |

DRAWING TITLE

EAST AND WEST ELEVATIONS

ICF elevations with openings, levels and roof build-up

|       |      |          |       |
|-------|------|----------|-------|
| SCALE | SIZE | DATE     | DRAWN |
| 1:150 | A3   | 23.09.26 | TS    |

|              |                 |     |
|--------------|-----------------|-----|
| STATUS       | DRAWING No.     | REV |
| FOR APPROVAL | UKPCS-003-EL-02 | P01 |