

Do not scale. All dimensions in mm. Check all dimensions on site.




- ICF wall at the plan cut (see the ICF sheet)
- Load-bearing masonry wall (context)
- Steel over (dashed), marked
- Steel column cut
- Engineer's pier bars (n-H12 vertical bars in ICF pier) | WS wall starters
- Section line (see SE sheet)

## GF STEEL OVER ICF

Scale 1:100 @ A2 | Plan cut at +1382



FOR APPROVAL - NOT FOR CONSTRUCTION

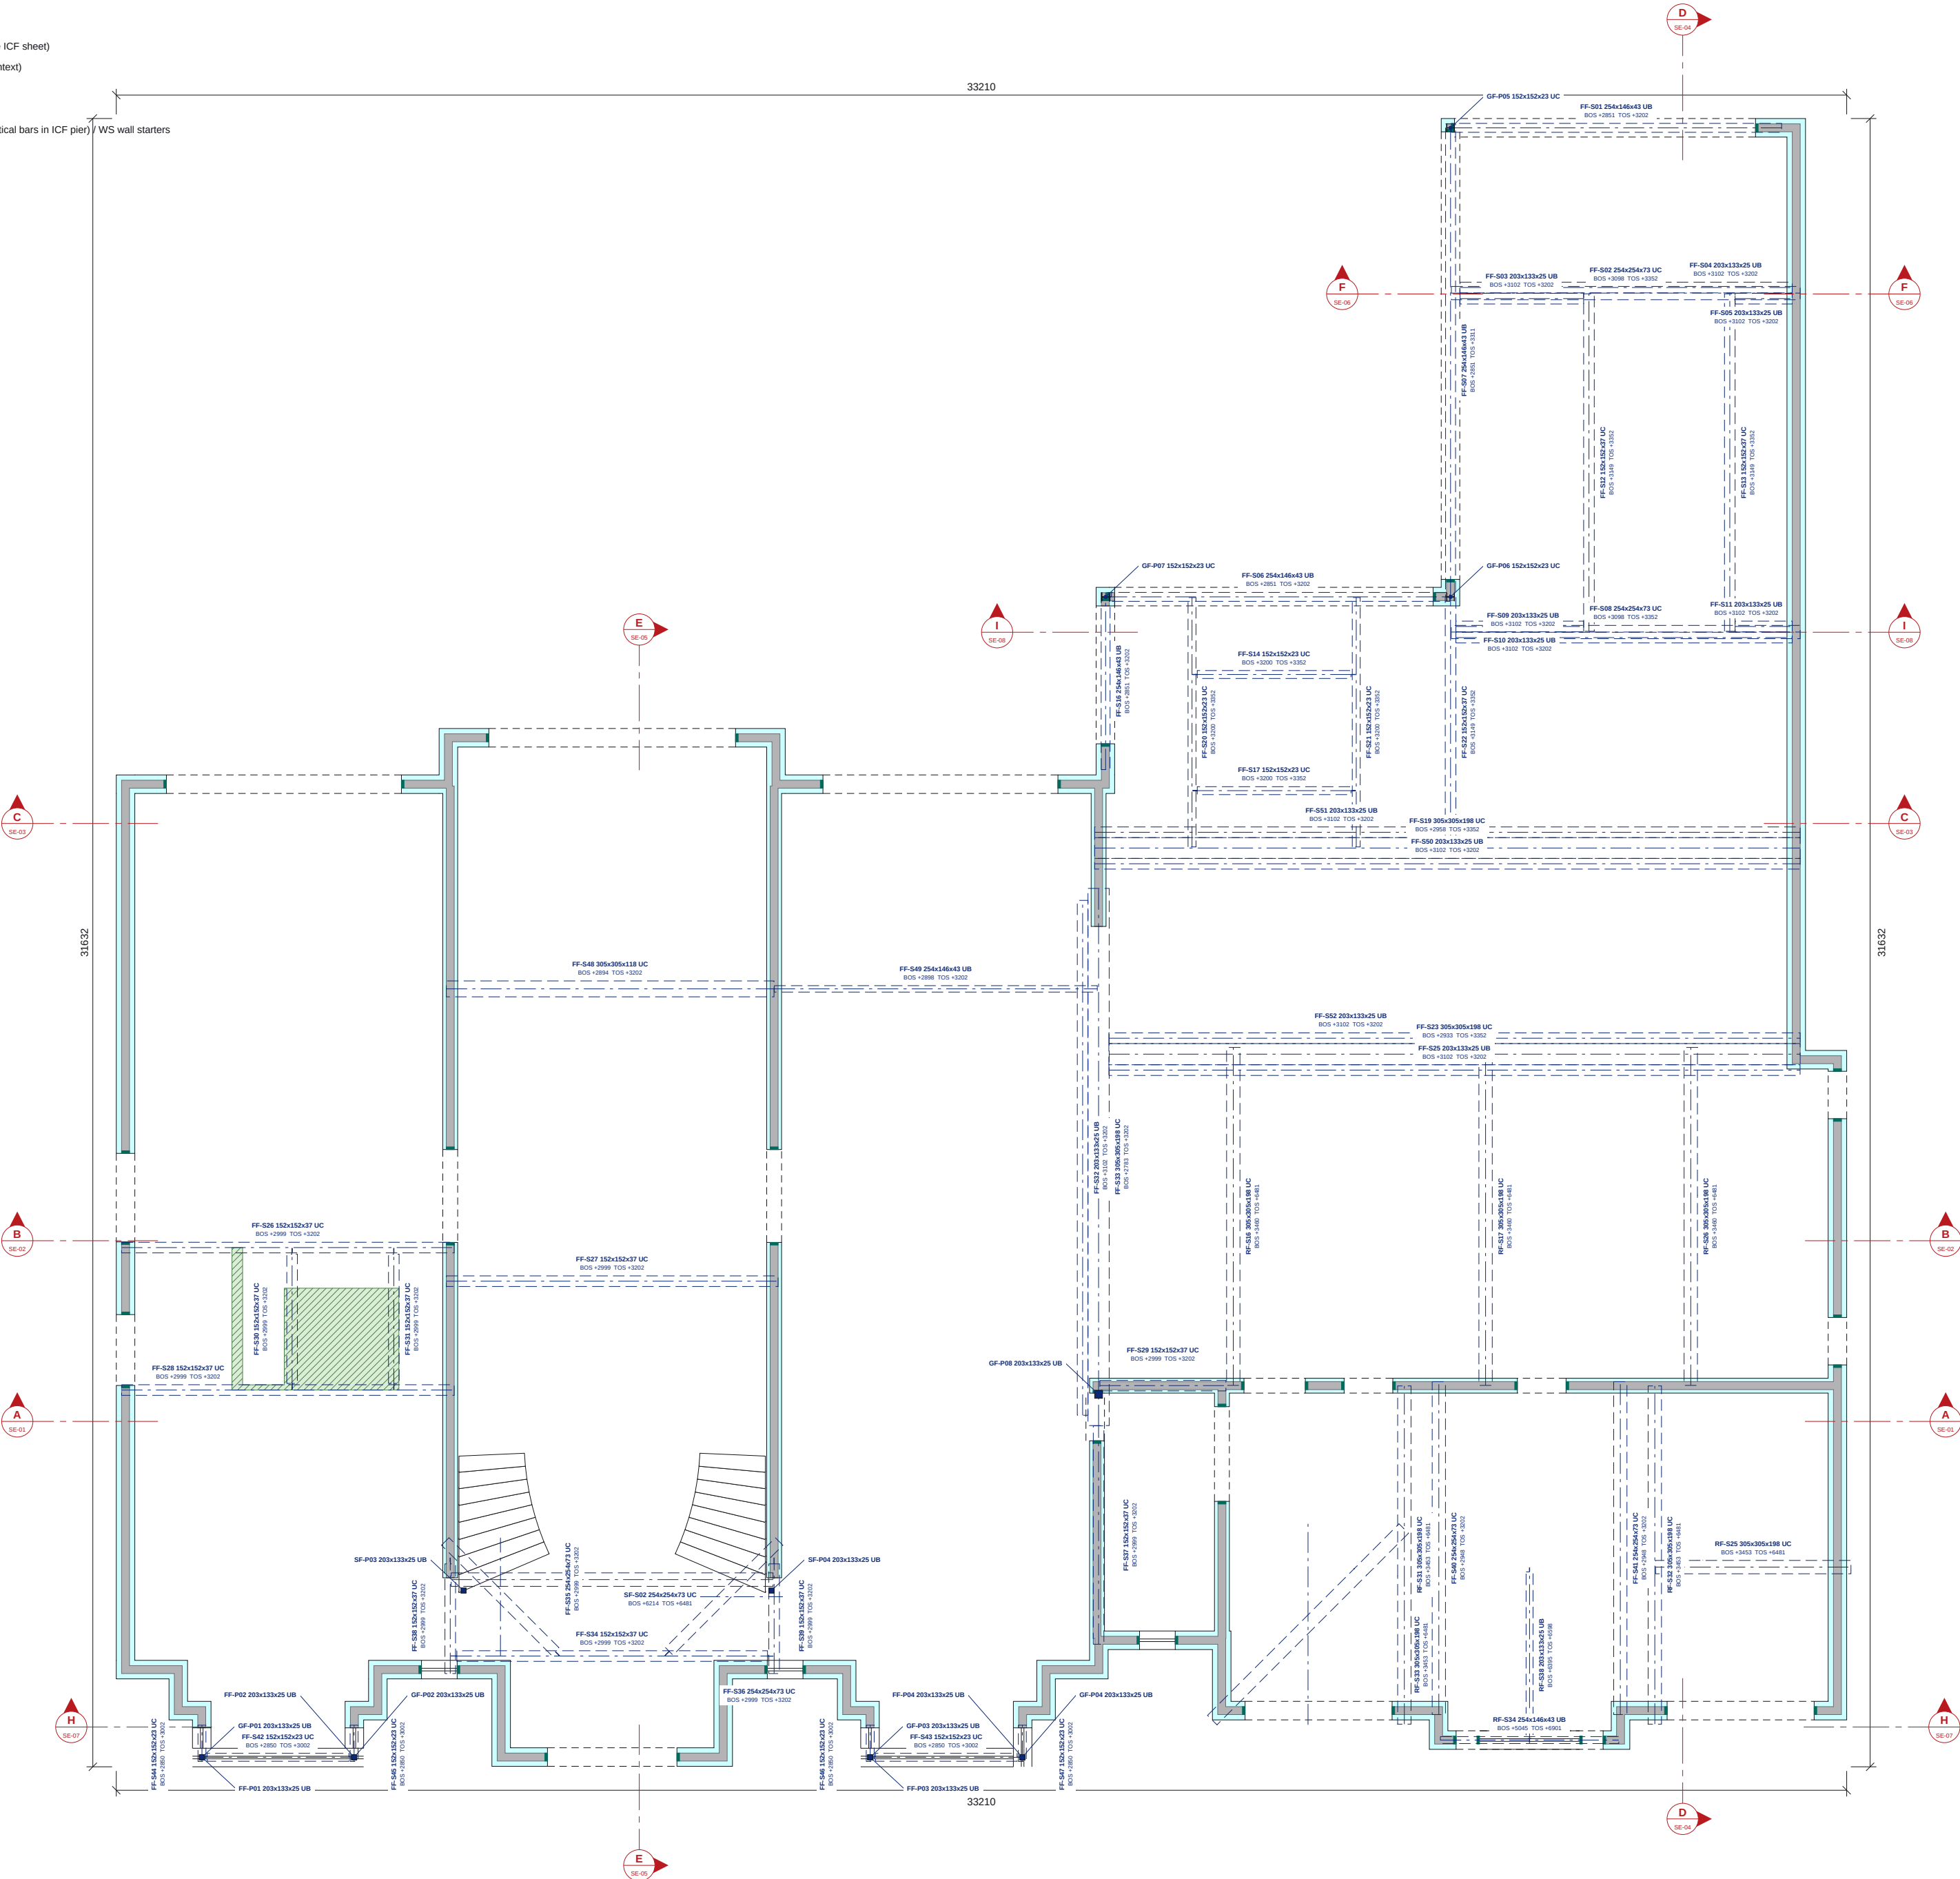

## GF STEEL SCHEDULE

| STEEL SCHEDULE |                     | BOS   | TOS   |
|----------------|---------------------|-------|-------|
| Mark           | Section (engineer)  |       |       |
| FF-S01         | 254x146x43 UB S355  | +2851 | +3202 |
| FF-S02         | 254x254x73 UC S355  | +3098 | +3352 |
| FF-S03         | 203x133x25 UB S355  | +3102 | +3202 |
| FF-S04         | 203x133x25 UB S355  | +3102 | +3202 |
| FF-S05         | 203x133x25 UB S355  | +3102 | +3202 |
| FF-S06         | 254x146x43 UB S355  | +2851 | +3202 |
| FF-S07         | 254x146x43 UB S355  | +2851 | +3311 |
| FF-S08         | 254x254x73 UC S355  | +3098 | +3352 |
| FF-S09         | 203x133x25 UB S355  | +3102 | +3202 |
| FF-S10         | 203x133x25 UB S355  | +3102 | +3202 |
| FF-S11         | 203x133x25 UB S355  | +3102 | +3202 |
| FF-S12         | 152x152x37 UC S355  | +3149 | +3352 |
| FF-S13         | 152x152x37 UC S355  | +3149 | +3352 |
| FF-S14         | 152x152x23 UC S355  | +3200 | +3352 |
| FF-S16         | 254x146x43 UB S355  | +2851 | +3202 |
| FF-S17         | 152x152x23 UC S355  | +3200 | +3352 |
| FF-S19         | 305x305x198 UC S355 | +2958 | +3352 |
| FF-S20         | 152x152x23 UC S355  | +3200 | +3352 |
| FF-S21         | 152x152x23 UC S355  | +3200 | +3352 |
| FF-S22         | 152x152x37 UC S355  | +3149 | +3352 |
| FF-S23         | 305x305x198 UC S355 | +2933 | +3352 |
| FF-S25         | 203x133x25 UB S355  | +3102 | +3202 |
| FF-S26         | 152x152x37 UC S355  | +2999 | +3202 |
| FF-S27         | 152x152x37 UC S355  | +2999 | +3202 |
| FF-S28         | 152x152x37 UC S355  | +2999 | +3202 |
| FF-S29         | 152x152x37 UC S355  | +2999 | +3202 |
| FF-S30         | 152x152x37 UC S355  | +2999 | +3202 |
| FF-S31         | 152x152x37 UC S355  | +2999 | +3202 |
| FF-S32         | 203x133x25 UB S355  | +3102 | +3202 |
| FF-S33         | 305x305x198 UC S355 | +2783 | +3202 |
| FF-S34         | 152x152x37 UC S355  | +2999 | +3202 |
| FF-S35         | 254x254x73 UC S355  | +2999 | +3202 |
| FF-S36         | 254x254x73 UC S355  | +2999 | +3202 |
| FF-S37         | 152x152x37 UC S355  | +2999 | +3202 |
| FF-S38         | 152x152x37 UC S355  | +2999 | +3202 |
| FF-S39         | 152x152x37 UC S355  | +2999 | +3202 |
| FF-S40         | 254x254x73 UC S355  | +2948 | +3202 |
| FF-S41         | 254x254x73 UC S355  | +2948 | +3202 |
| FF-S42         | 152x152x23 UC S355  | +2850 | +3002 |
| FF-S43         | 152x152x23 UC S355  | +2850 | +3002 |
| FF-S44         | 152x152x23 UC S355  | +2850 | +3002 |
| FF-S45         | 152x152x23 UC S355  | +2850 | +3002 |
| FF-S46         | 152x152x23 UC S355  | +2850 | +3002 |
| FF-S47         | 152x152x23 UC S355  | +2850 | +3002 |
| FF-S48         | 305x305x118 UC S355 | +2894 | +3202 |
| FF-S49         | 254x146x43 UB S355  | +2898 | +3202 |
| FF-S50         | 203x133x25 UB S355  | +3102 | +3202 |
| FF-S51         | 203x133x25 UB S355  | +3102 | +3202 |
| FF-S52         | 203x133x25 UB S355  | +3102 | +3202 |
| RF-S16         | 305x305x198 UC S355 | +3460 | +6481 |
| RF-S17         | 305x305x198 UC S355 | +3460 | +6481 |
| RF-S25         | 305x305x198 UC S355 | +3453 | +6481 |
| RF-S26         | 305x305x198 UC S355 | +3460 | +6481 |
| RF-S31         | 305x305x198 UC S355 | +3453 | +6481 |
| RF-S32         | 305x305x198 UC S355 | +3453 | +6481 |
| RF-S33         | 305x305x198 UC S355 | +3453 | +6481 |
| RF-S34         | 254x146x43 UB S355  | +5045 | +6901 |
| RF-S38         | 203x133x25 UB S355  | +6395 | +6996 |
| SF-S02         | 254x254x73 UC S355  | +6214 | +6481 |
| FF-P01         | 203x133x25 UB S355  | +3352 | +5925 |
| FF-P02         | 203x133x25 UB S355  | +3352 | +5925 |
| FF-P03         | 203x133x25 UB S355  | +3352 | +5925 |
| FF-P04         | 203x133x25 UB S355  | +3352 | +5925 |
| GF-P01         | 203x133x25 UB S355  | -98   | +2850 |
| GF-P02         | 203x133x25 UB S355  | -98   | +2850 |
| GF-P03         | 203x133x25 UB S355  | -98   | +2850 |
| GF-P04         | 203x133x25 UB S355  | -98   | +2850 |
| GF-P05         | 152x152x23 UC S355  | -98   | +2851 |
| GF-P06         | 152x152x23 UC S355  | -98   | +2851 |
| GF-P07         | 152x152x23 UC S355  | -98   | +2851 |
| GF-P08         | 203x133x25 UB S355  | -98   | +2783 |
| SF-P03         | 203x133x25 UB S355  | +6481 | +7559 |
| SF-P04         | 203x133x25 UB S355  | +6481 | +7559 |

BOS / TOS = bottom / top of steel above GF FFL (C-1 columns: base / top).

## NOTES

- ICF per the coordinated model: 6in XR35 (152 mm core, 355.6 mm) external walls, 6in Std (286 mm) internal ICF walls; concrete grade, aggregate, fibre dosage and dowel bars per the Tier Consult specification (to be confirmed).
- Lintel (L-n) and steel (B-n, C-1) marks from Tier Consult 078-TCE-DEN-XX-DR-S-096.210 rev -, which takes precedence. Red EQ tags = queries to the engineer on UKPCS-003-EQ-01 (click to open).
- Masonry walls shown for context.
- Steel over dashed. BOS / TOS = bottom / top of steel above GF FFL.
- Steel over the ICF at this level, dashed, with the engineer's member marks as modelled; BOS / TOS = bottom / top of steel above GF FFL. Columns cut at the plan level shown solid.
- Walls and openings: see UKPCS-003-GA-01 for the ICF setting out, opening sizes and the opening schedule.
- No structural grid is registered on this issue.

## REVISIONS

| REV | DATE     | DESCRIPTION    |
|-----|----------|----------------|
| P01 | 23.09.26 | Approval issue |



|           |          |
|-----------|----------|
| CLIENT    | PROJECT  |
| ICF Homes | Dendrons |

## DRAWING TITLE

### GF STEEL OVER ICF

Steel over the ICF, marked and scheduled

|       |      |          |       |
|-------|------|----------|-------|
| SCALE | SIZE | DATE     | DRAWN |
| 1:100 | A2   | 23.09.26 | TS    |

|        |             |     |
|--------|-------------|-----|
| STATUS | DRAWING No. | REV |
|--------|-------------|-----|

FOR APPROVAL

UKPCS-003-GS-01

P01