




FOR APPROVAL - NOT FOR CONSTRUCTION

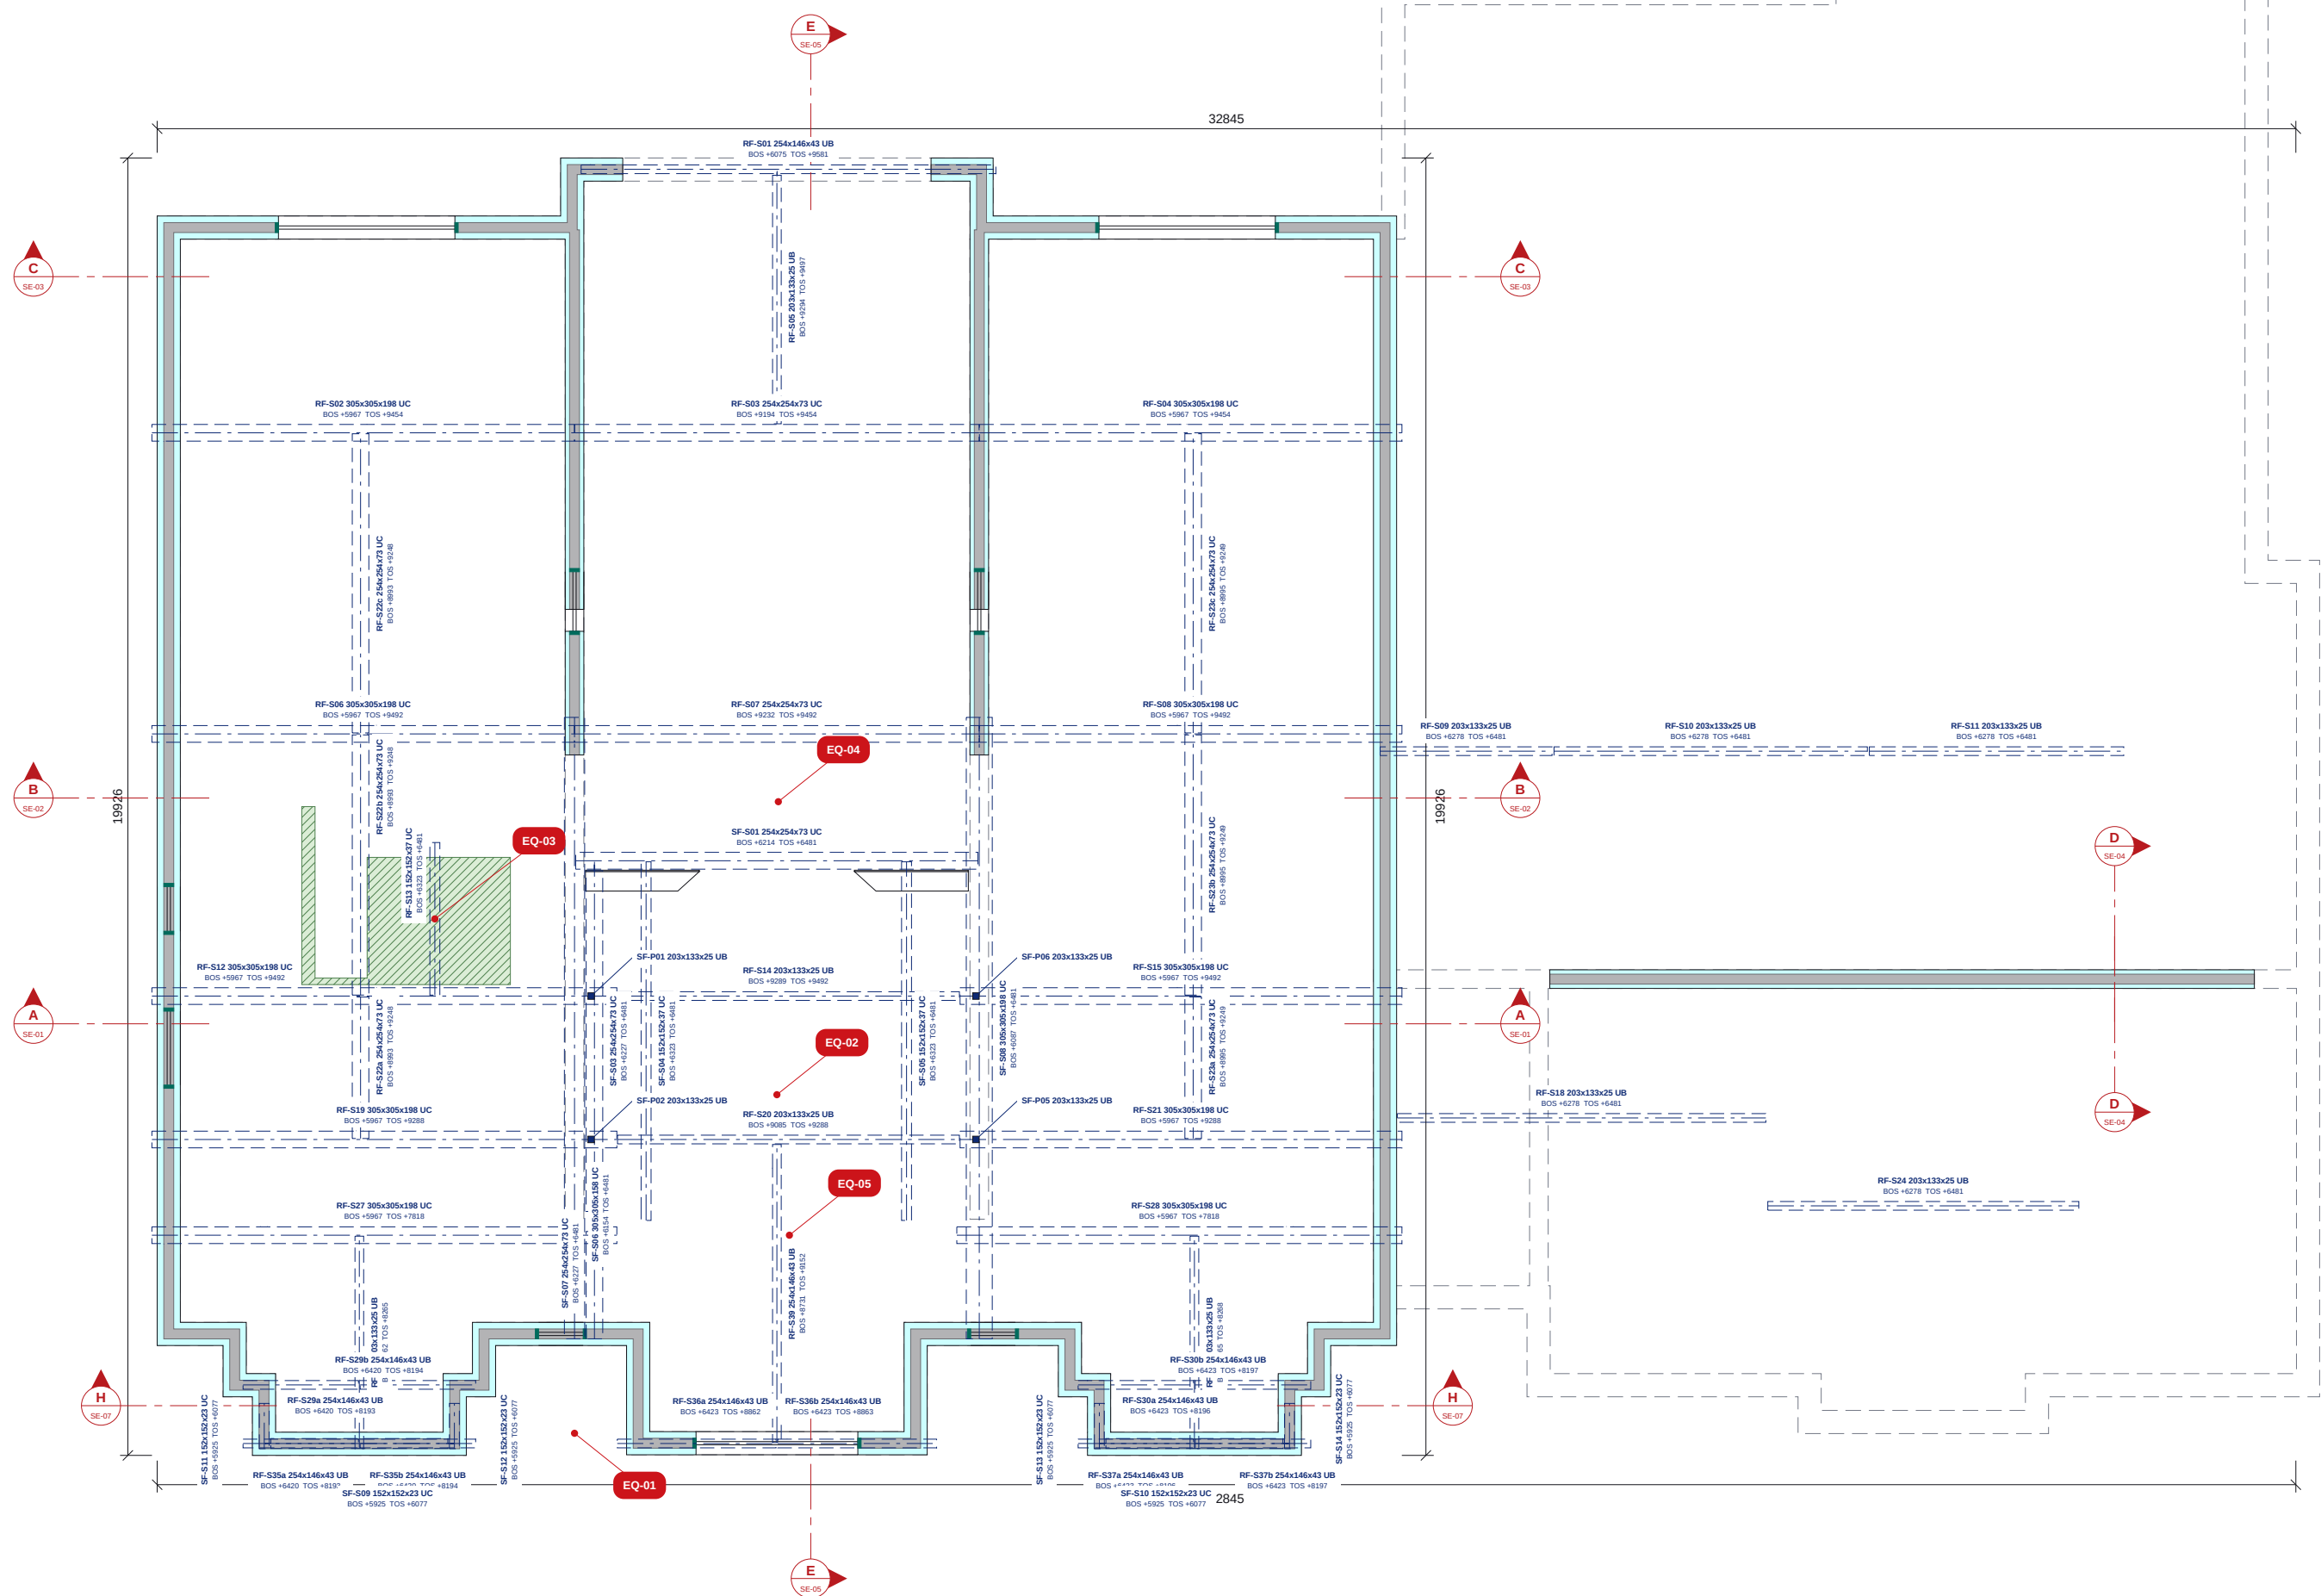

FF STEEL OVER ICF

Scale 1:100 @ A2 | Plan cut at +237

FF STEEL SCHEDULE

STEEL SCHEDULE

Mark	Section (engineer)	BOS	TOS
RF-S01	254x146x43 UB S355	+6075	+9581
RF-S02	305x305x198 UC S355	+5967	+9454
RF-S03	254x254x73 UC S355	+9194	+9454
RF-S04	305x305x198 UC S355	+5967	+9454
RF-S05	203x133x25 UB S355	+9294	+9497
RF-S06	305x305x198 UC S355	+5967	+9492
RF-S07	254x254x73 UC S355	+9232	+9492
RF-S08	305x305x198 UC S355	+5967	+9492
RF-S09	203x133x25 UB S355	+6278	+6481
RF-S10	203x133x25 UB S355	+6278	+6481
RF-S11	203x133x25 UB S355	+6278	+6481
RF-S12	305x305x198 UC S355	+5967	+9492
RF-S13	152x152x37 UC S355	+6323	+6481
RF-S14	203x133x25 UB S355	+9289	+9492
RF-S15	305x305x198 UC S355	+5967	+9492
RF-S18	203x133x25 UB S355	+6278	+6461
RF-S19	305x305x198 UC S355	+5967	+9288
RF-S20	203x133x25 UB S355	+9085	+9288
RF-S21	305x305x198 UC S355	+5967	+9288
RF-S22a	254x254x73 UC S355	+8993	+9248
RF-S22b	254x254x73 UC S355	+8993	+9248
RF-S22c	254x254x73 UC S355	+8993	+9248
RF-S23a	254x254x73 UC S355	+8995	+9249
RF-S23b	254x254x73 UC S355	+8995	+9249
RF-S23c	254x254x73 UC S355	+8995	+9249
RF-S24	203x133x25 UB S355	+6278	+6481
RF-S27	305x305x198 UC S355	+5967	+7818
RF-S28	305x305x198 UC S355	+5967	+7818
RF-S29a	254x146x43 UB S355	+6420	+8193
RF-S29b	254x146x43 UB S355	+6420	+8194
RF-S30a	254x146x43 UB S355	+6423	+8196
RF-S30b	254x146x43 UB S355	+6423	+8197
RF-S35a	254x146x43 UB S355	+6420	+8193
RF-S35b	254x146x43 UB S355	+6420	+8194
RF-S36a	254x146x43 UB S355	+6423	+8862
RF-S36b	254x146x43 UB S355	+6423	+8863
RF-S37a	254x146x43 UB S355	+6423	+8196
RF-S37b	254x146x43 UB S355	+6423	+8197
RF-S39	254x146x43 UB S355	+8731	+9152
RF-S40	203x133x25 UB S355	+8062	+8265
RF-S41	203x133x25 UB S355	+8065	+8268
SF-S01	254x254x73 UC S355	+6214	+6481
SF-S03	254x254x73 UC S355	+6227	+6481
SF-S04	152x152x37 UC S355	+6323	+6481
SF-S05	152x152x37 UC S355	+6323	+6481
SF-S06	305x305x158 UC S355	+6154	+6481
SF-S07	254x254x73 UC S355	+6227	+6481
SF-S08	305x305x198 UC S355	+6087	+6481
SF-S09	152x152x23 UC S355	+5925	+6077
SF-S10	152x152x23 UC S355	+5925	+6077
SF-S11	152x152x23 UC S355	+5925	+6077
SF-S12	152x152x23 UC S355	+5925	+6077
SF-S13	152x152x23 UC S355	+5925	+6077
SF-S14	152x152x23 UC S355	+5925	+6077
SF-P01	203x133x25 UB S355	+6481	+9232
SF-P02	203x133x25 UB S355	+6481	+9029
SF-P05	203x133x25 UB S355	+6481	+9029
SF-P06	203x133x25 UB S355	+6481	+9232

BOS / TOS = bottom / top of steel above GF FFL (C-1 columns: base / top).

NOTES

- ICF per the coordinated model: 6in XR35 (152 mm core, 355.6 mm) external walls, 6in Std (286 mm) internal ICF walls; concrete grade, aggregate, fibre dosage and dowel bars per the Tier Consult specification (to be confirmed).
- Lintel (L-n) and steel (B-n, C-1) marks from Tier Consult 078-TCE-DEN-XX-DR-S-096.210 rev -, which takes precedence. Red EQ tags = queries to the engineer on UKPCS-003-EQ-01 (click to open).
- Masonry walls shown for context.
- Steel over dashed. BOS / TOS = bottom / top of steel above GF FFL.
- Steel over the ICF at this level, dashed, with the engineer's member marks as modelled: BOS / TOS = bottom / top of steel above GF FFL. Columns cut at the plan level shown solid.
- Walls and openings: see UKPCS-003-GA-02 for the ICF setting out, opening sizes and the opening schedule.
- No structural grid is registered on this issue.

REVISIONS

REV	DATE	DESCRIPTION
P01	23.09.26	Approval issue



CLIENT

ICF Homes

PROJECT

Dendrons

DRAWING TITLE

FF STEEL OVER ICF

Steel over the ICF, marked and scheduled

SCALE

1:100

SIZE

A2

DATE

23.09.26

DRAWN

TS

STATUS

FOR APPROVAL

DRAWING No.

UKPCS-003-GS-02

REV

P01