



FOR APPROVAL - NOT FOR CONSTRUCTION

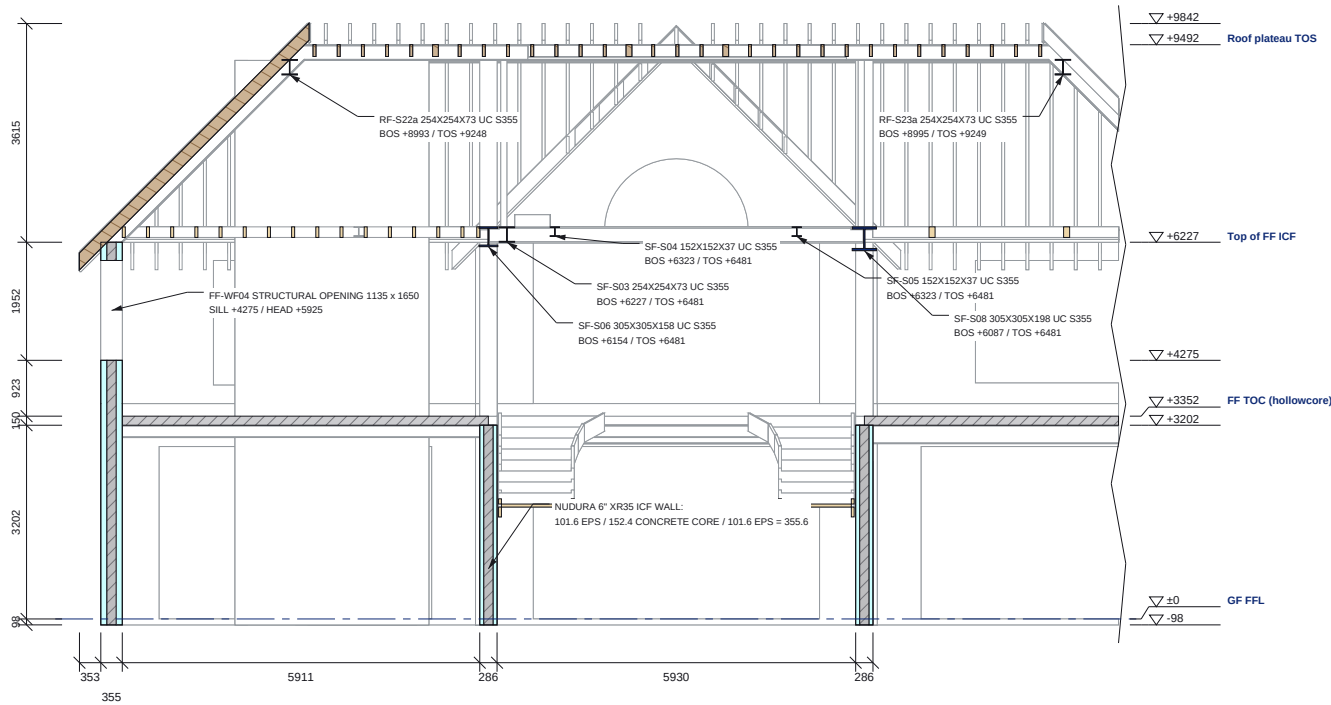

SECTION A-A (PART 1 OF 2)

Scale 1:125 @ A3 | Looking north; levels above GF FFL

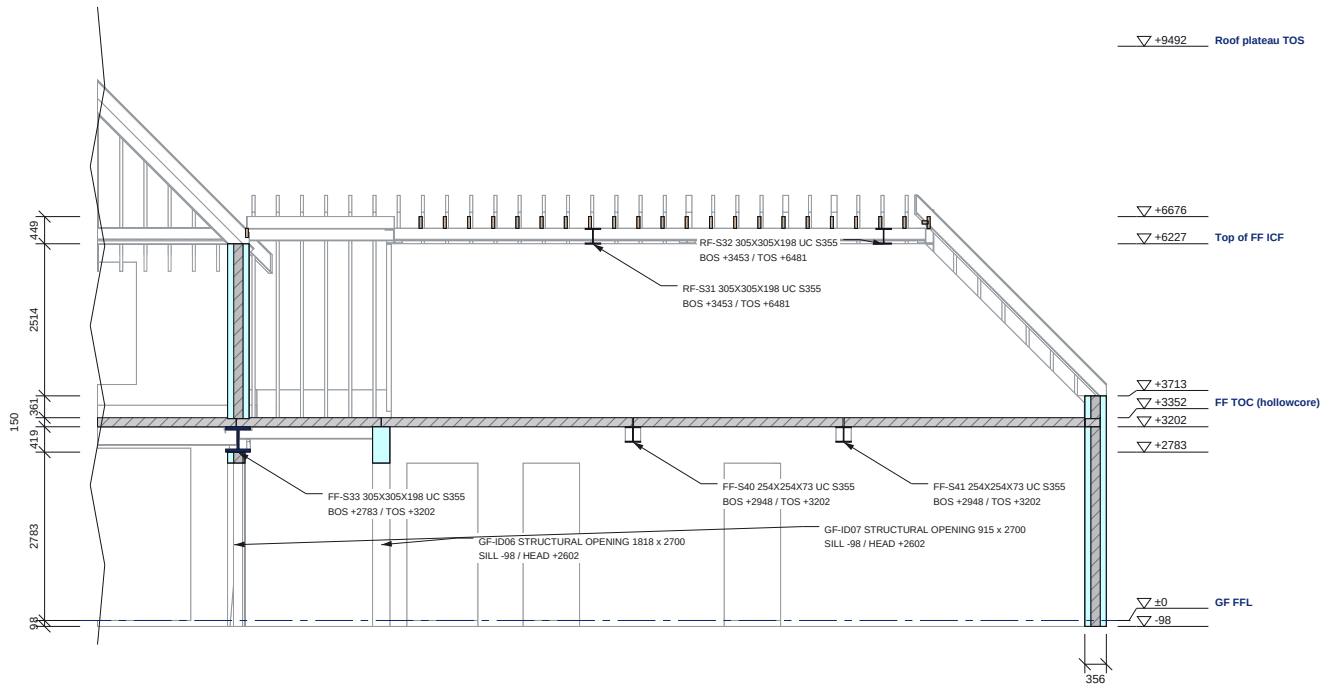

SECTION A-A (PART 2 OF 2)

Scale 1:125 @ A3 | Looking north; levels above GF FFL

- Legend:
- ICF EPS (cut)
 - ICF concrete core / RC (cut)
 - Steel (cut)
 - Masonry wall (cut)
 - Beyond the cut (line work)



SECTION A-A SCHEDULES


LEVELS ON THIS SECTION

Level	FFL	AOD
underside of ICF	-98	168.650
GF FFL	0	168.748
top of ICF	+2783	171.531
top of ICF	+3202	171.950
FF TOC (hollowcore)	+3352	172.100
top of ICF	+3713	172.461
top of ICF	+4275	173.023
Top of FF ICF	+6227	174.975
top of roof build-up	+6676	175.424
Roof plateau TOS	+9492	178.240
top of roof build-up	+9842	178.590

STEEL CUT BY THIS SECTION

Mark	Section (engineer)	BOS	TOS
FF-S33	305x305x198 UC S355	+2783	+3202
FF-S40	254x254x73 UC S355	+2948	+3202
FF-S41	254x254x73 UC S355	+2948	+3202
RF-S31	305x305x198 UC S355	+3453	+6481
RF-S32	305x305x198 UC S355	+3453	+6481
RF-S22a	254x254x73 UC S355	+8993	+9248
RF-S23a	254x254x73 UC S355	+8995	+9249
SF-S03	254x254x73 UC S355	+6227	+6481
SF-S04	152x152x37 UC S355	+6323	+6481
SF-S05	152x152x37 UC S355	+6323	+6481
SF-S06	305x305x158 UC S355	+6154	+6481
SF-S08	305x305x198 UC S355	+6087	+6481

SECTION KEY

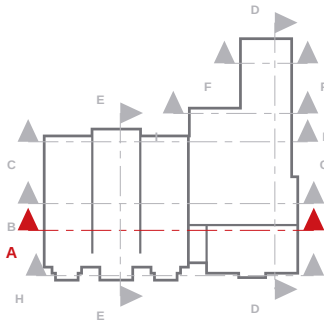

NOTES

- Section A-A is a BuildEase ICF section (not an architect's section line). Cut elements hatched / filled; the model beyond the cut in line work.
- Levels above GF FFL (168.748 AOD); the level table gives AOD.
- ICF: Nudura 6" XR35, 101.6 EPS + 152.4 core + 101.6 EPS = 355.6; 6" Std, 66.7 EPS + 152.4 core + 66.7 EPS = 285.8, 152.4 core + 101.6 EPS = 355.6. ICF per the coordinated model: 6in XR35 (152 mm core, 355.6 mm) external walls, 6in Std (286 mm) internal ICF walls; concrete grade, aggregate, fibre dosage and dowel bars per the Tier Consult specification (to be confirmed).
- Steel marks, BOS / TOS: Tier Consult 078-TCE-DEN-XX-DR-S-096..210 rev -. See UKPCS-003-GA-01 / EL-01 / EL-02.

REVISIONS

REV	DATE	DESCRIPTION
P01	23.09.26	Approval issue



CLIENT	PROJECT
ICF Homes	Dendrons

DRAWING TITLE

SECTION A-A

ICF section with levels and build-ups

SCALE	SIZE	DATE	DRAWN
1:125	A3	23.09.26	TS
STATUS		DRAWING No.	
FOR APPROVAL		UKPCS-003-SE-01	REV
			P01