



FOR APPROVAL - NOT FOR CONSTRUCTION

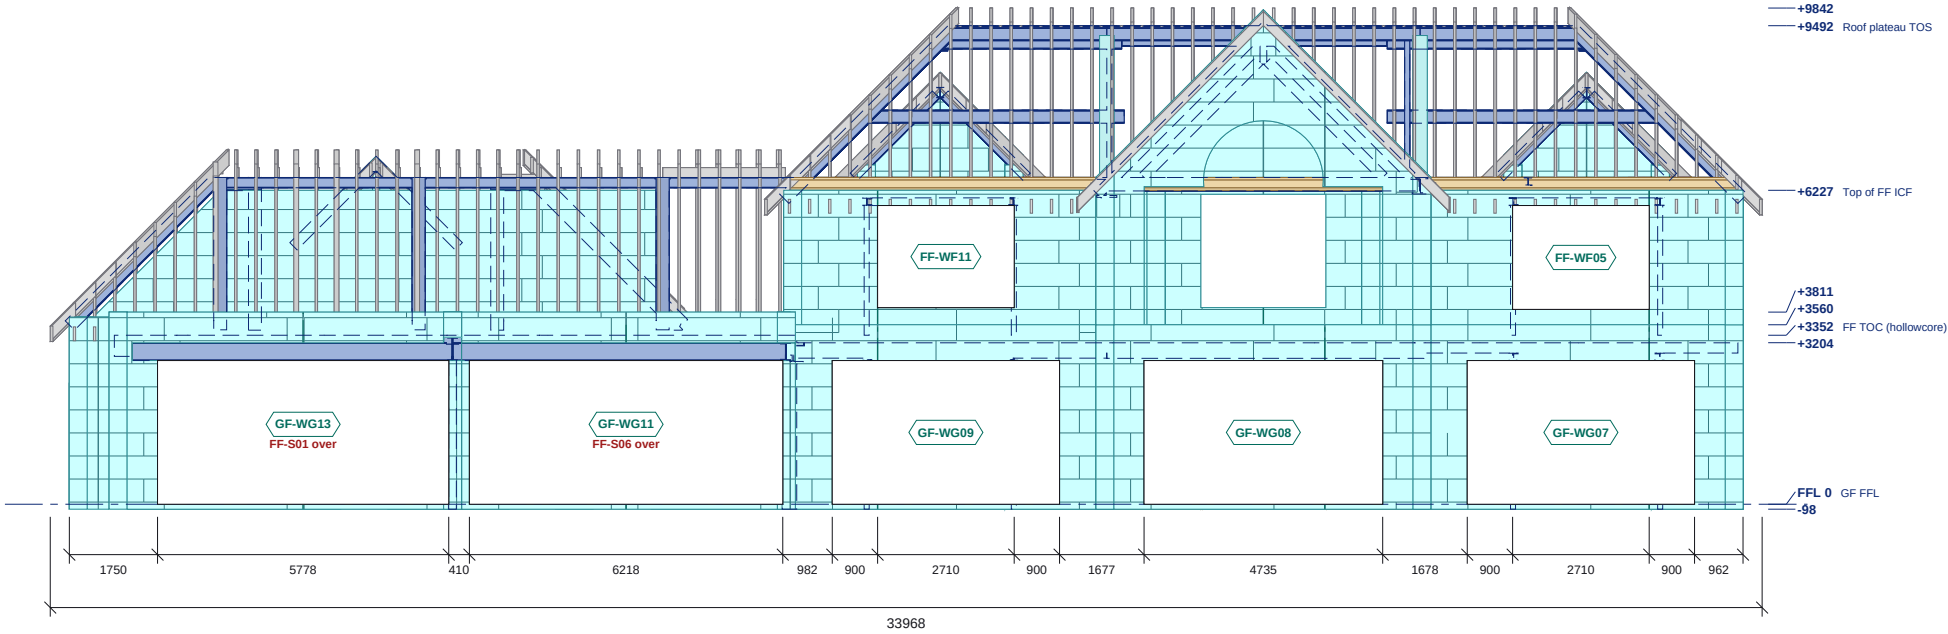


NORTH ELEVATION

Scale 1:150 @ A3 | Levels above GF FFL (AOD in the schedule); sills and heads in the schedule

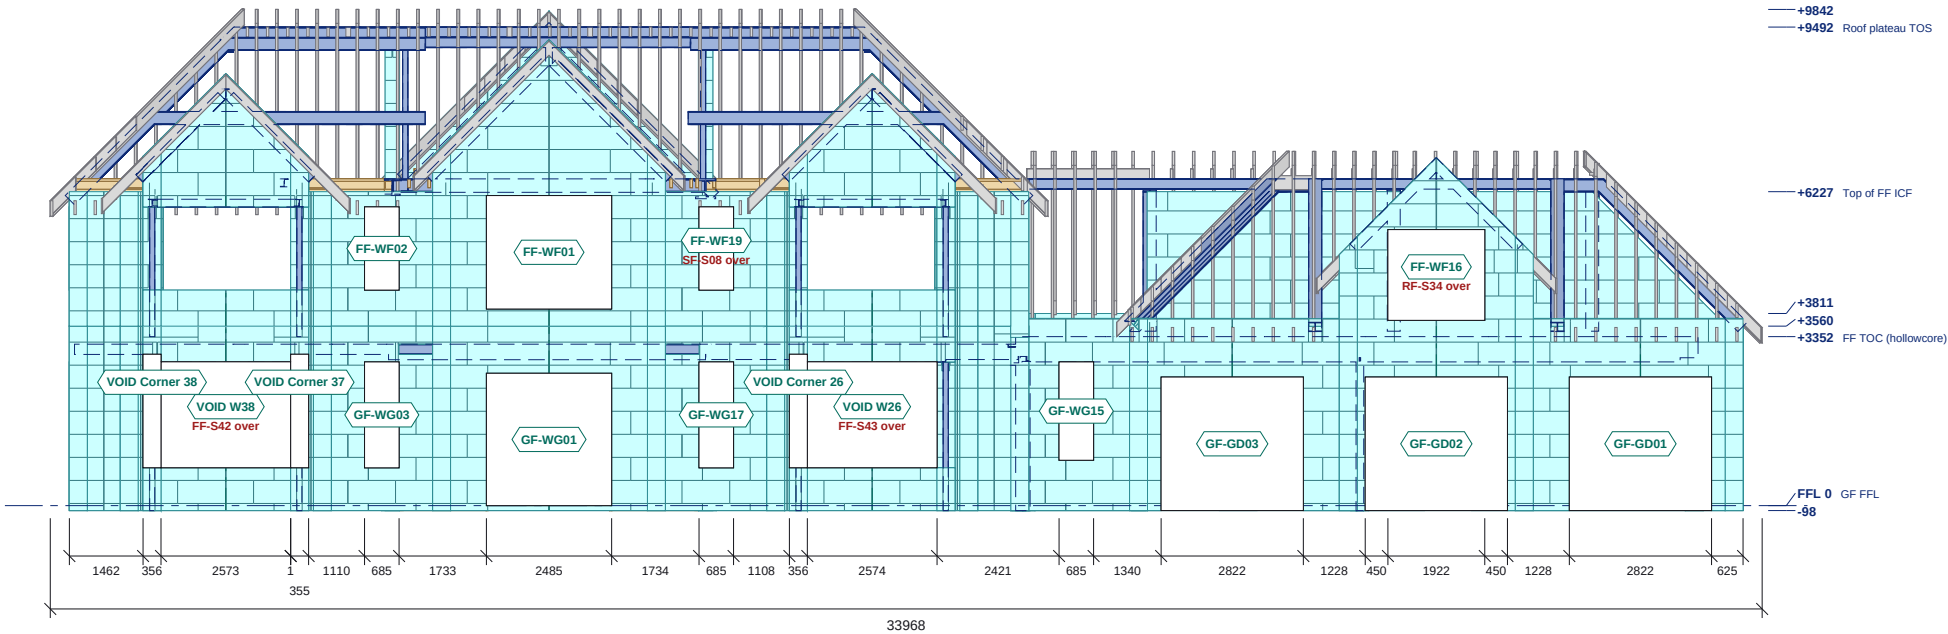

SOUTH ELEVATION

Scale 1:150 @ A3 | Levels above GF FFL (AOD in the schedule); sills and heads in the schedule

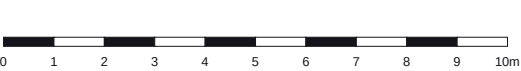

- ICF external EPS face
- Block course joint
- Stack joint
- Steel
- Roof build-up (slab / earth / sedum)

ELEVATION SCHEDULES

NORTH ELEVATION: OPENINGS

Ref	Width	Height	Sill	Head	Lintel
FF-WF05	2710	2060	+3865	+5925	-
FF-WF11	2710	2025	+3900	+5925	-
GF-WG07	4510	2850	0	+2850	-
GF-WG08	4735	2850	0	+2850	-
GF-WG09	4510	2850	0	+2850	-
GF-WG11	6218	2850	0	+2850	FF-S06 over
GF-WG13	5778	2850	0	+2850	FF-S01 over

Structural openings in the ICF; sill and head above GF FFL.

SOUTH ELEVATION: OPENINGS

Ref	Width	Height	Sill	Head	Lintel
FF-WF01	2485	2250	+3900	+6150	-
FF-WF02	685	1650	+4275	+5925	-
FF-WF16	1922	1800	+3675	+5475	RF-S34 over
FF-WF19	685	1650	+4275	+5925	SF-S08 over
GF-GD01	2822	2648	-98	+2550	-
GF-GD02	2822	2648	-98	+2550	-
GF-GD03	2822	2648	-98	+2550	-
GF-WG01	2485	2625	0	+2625	-
GF-WG03	685	2100	+750	+2850	-
GF-WG15	685	1950	+900	+2850	-
GF-WG17	685	2100	+750	+2850	-
VOID Corner 26	356	2250	+752	+3002	-
VOID Corner 37	356	2250	+752	+3002	-
VOID Corner 38	356	2250	+752	+3002	-
VOID W26	2574	2100	+752	+2852	FF-S43 over
VOID W38	2574	2100	+752	+2852	FF-S42 over

Structural openings in the ICF; sill and head above GF FFL.

LEVELS ON THESE ELEVATIONS

Level	FFL	AOD
underside of ICF	-98	168.650
GF FFL	0	168.748
top of ICF	+3204	171.952
FF TOC (hollowcore)	+3352	172.100
top of ICF	+3560	172.308
top of ICF	+3811	172.559
Top of FF ICF	+6227	174.975
Roof plateau TOS	+9492	178.240
top of roof build-up	+9842	178.590

NOTES

- ICF: Nudura 6" XR35, 101.6 EPS + 152.4 core + 101.6 EPS = 355.6; 6" Std, 66.7 EPS + 152.4 core + 66.7 EPS = 285.8. External EPS face shown with the block course joints, vertical block joints and stack joints as populated.
- Levels above GF FFL (168.748 AOD). Openings are structural openings in the ICF; glazing, doors, render and finishes by others, not shown.
- Steel and roof build-up shown as modelled.
- See UKPCS-003-GA-01 for plan setting out, lintels and steel.

REVISIONS

REV	DATE	DESCRIPTION
P01	23.09.26	Approval issue



CLIENT	PROJECT
ICF Homes	Dendrons

DRAWING TITLE

NORTH AND SOUTH ELEVATIONS

ICF elevations with openings, levels and roof build-up

SCALE	SIZE	DATE	DRAWN
1:150	A3	23.09.26	TS

STATUS	DRAWING No.	REV
FOR APPROVAL	UKPCS-003-EL-01	P01