

Do not scale. All dimensions in mm. Check all dimensions on site.




GF ICF PLAN

Scale 1:100 @ A2 | Plan cut at +1382



FOR APPROVAL - NOT FOR CONSTRUCTION

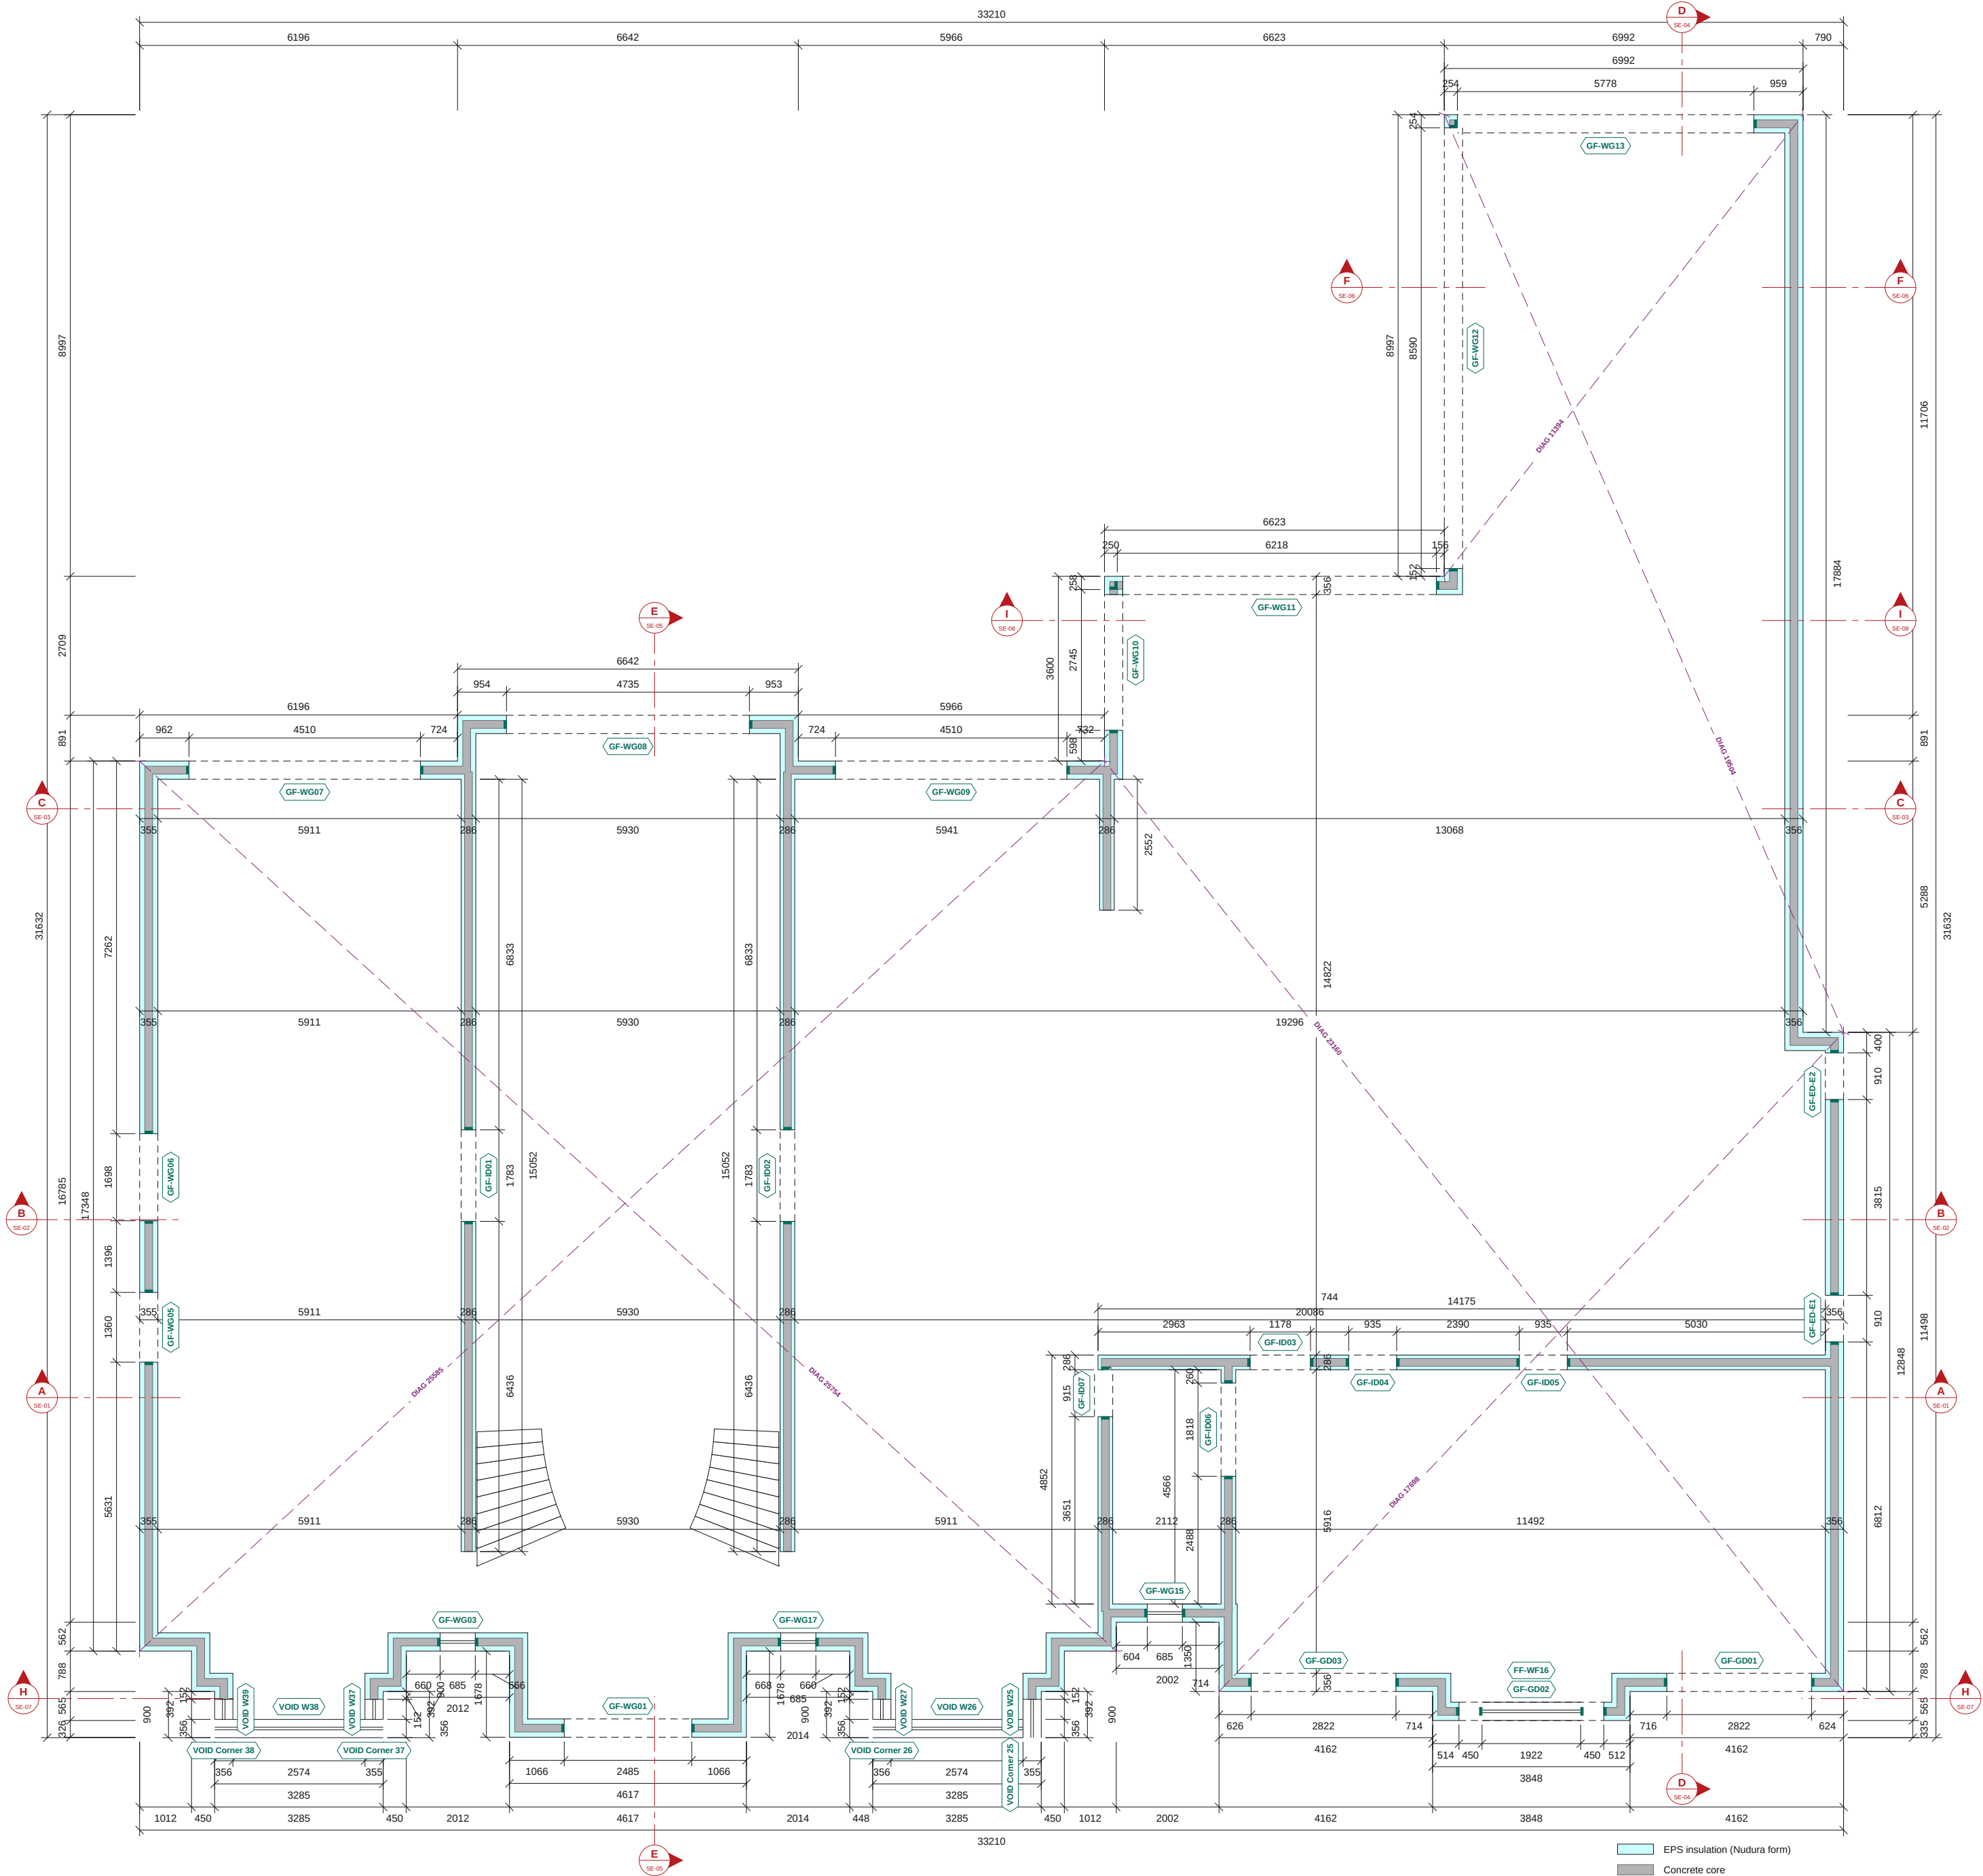

- EPS insulation (Nudura form)
- Concrete core
- End cap at opening
- Engineer's pier bars (n-H12 vertical bars in ICF pier) / WS wall starters
- Setting-out check diagonal (external ICF corners)
- Section line (see SE sheet)

GF ICF SCHEDULES

OPENING SCHEDULE

Ref	Width	Height	Sill	Head	Lintel
FF-WF16	1922	1800	+3675	+5475	-
GF-ED-E1	910	2400	0	+2400	-
GF-ED-E2	910	2400	0	+2400	-
GF-GD01	2822	2648	-98	+2550	-
GF-GD02	2822	2648	-98	+2550	-
GF-GD03	2822	2648	-98	+2550	-
GF-ID01	1783	2700	-98	+2602	-
GF-ID02	1783	2700	-98	+2602	-
GF-ID03	1178	2700	-98	+2602	-
GF-ID04	935	2700	-98	+2602	-
GF-ID05	935	2700	-98	+2602	-
GF-ID06	1818	2700	-98	+2602	-
GF-ID07	915	2700	-98	+2602	-
GF-WG01	2485	2625	0	+2625	-
GF-WG03	685	2100	+750	+2850	-
GF-WG05	1360	2850	0	+2850	-
GF-WG06	1698	2850	0	+2850	-
GF-WG07	4510	2850	0	+2850	-
GF-WG08	4735	2850	0	+2850	-
GF-WG09	4510	2850	0	+2850	-
GF-WG10	2745	2850	0	+2850	-
GF-WG11	6218	2850	0	+2850	-
GF-WG12	8590	2850	0	+2850	-
GF-WG13	5778	2850	0	+2850	-
GF-WG15	685	1950	+900	+2850	-
GF-WG17	685	2100	+750	+2850	-
VOID Corner 25	356	2250	+752	+3002	-
VOID Corner 26	356	2250	+752	+3002	-
VOID Corner 37	356	2250	+752	+3002	-
VOID Corner 38	356	2250	+752	+3002	-
VOID W25	392	2250	+752	+3002	-
VOID W26	2574	2100	+752	+2852	-
VOID W27	392	2250	+752	+3002	-
VOID W37	392	2250	+752	+3002	-
VOID W38	2574	2100	+752	+2852	-
VOID W39	392	2250	+752	+3002	-

Structural openings in the ICF, sill and head above GF FFL. VOID = subtract cut in the ICF (no end caps / lintel buck modelled).

NOTES

- ICF: Nudura 6" XR35, 101.6 EPS + 152.4 core + 101.6 EPS = 355.6; 6" Std, 66.7 EPS + 152.4 core + 66.7 EPS = 285.8. Dimensions to the ICF faces.
- Levels above GF FFL (168.748 AOD). Sill / head = structural opening in the ICF.
- ICF per the coordinated model: 6in XR35 (152 mm core, 355.6 mm) external walls, 6in Std (286 mm) internal ICF walls: concrete grade, aggregate, fibre dosage and dowel bars per the Tier Consult specification (to be confirmed).
- Lintel (L-n) and steel (B-n, C-1) marks from Tier Consult 078-TCE-DEN-XX-DR-S-096.210 rev -, which takes precedence. Red EQ tags = queries to the engineer on UKPCS-003-EQ-01 (click to open).
- Masonry walls shown for context.
- Steel over the ICF: see UKPCS-003-GS-01.

REVISIONS

REV	DATE	DESCRIPTION
P01	23.09.26	Approval issue



CLIENT ICF Homes	PROJECT Dendrons
---------------------	---------------------

DRAWING TITLE
GF ICF GENERAL ARRANGEMENT

ICF walls, openings and setting out

SCALE 1:100	SIZE A2	DATE 23.09.26	DRAWN TS
----------------	------------	------------------	-------------

STATUS FOR APPROVAL	DRAWING No. UKPCS-003-GA-01	REV P01
----------------------------	------------------------------------	----------------