




FOR APPROVAL - NOT FOR CONSTRUCTION

FF ICF SCHEDULES

OPENING SCHEDULE

Ref	Width	Height	Sill	Head	Lintel
FF-ID01	915	2400	+3352	+5752	-
FF-ID02	915	2400	+3352	+5752	-
FF-WF01	2485	2250	+3900	+6150	-
FF-WF02	685	1650	+4275	+5925	-
FF-WF04	1135	1650	+4275	+5925	-
FF-WF05	2710	2060	+3865	+5925	-
FF-WF11	2710	2025	+3900	+5925	-
FF-WF19	685	1650	+4275	+5925	-
FF-WF20	685	1650	+4275	+5925	-

Structural openings in the ICF; sill and head above GF FFL.

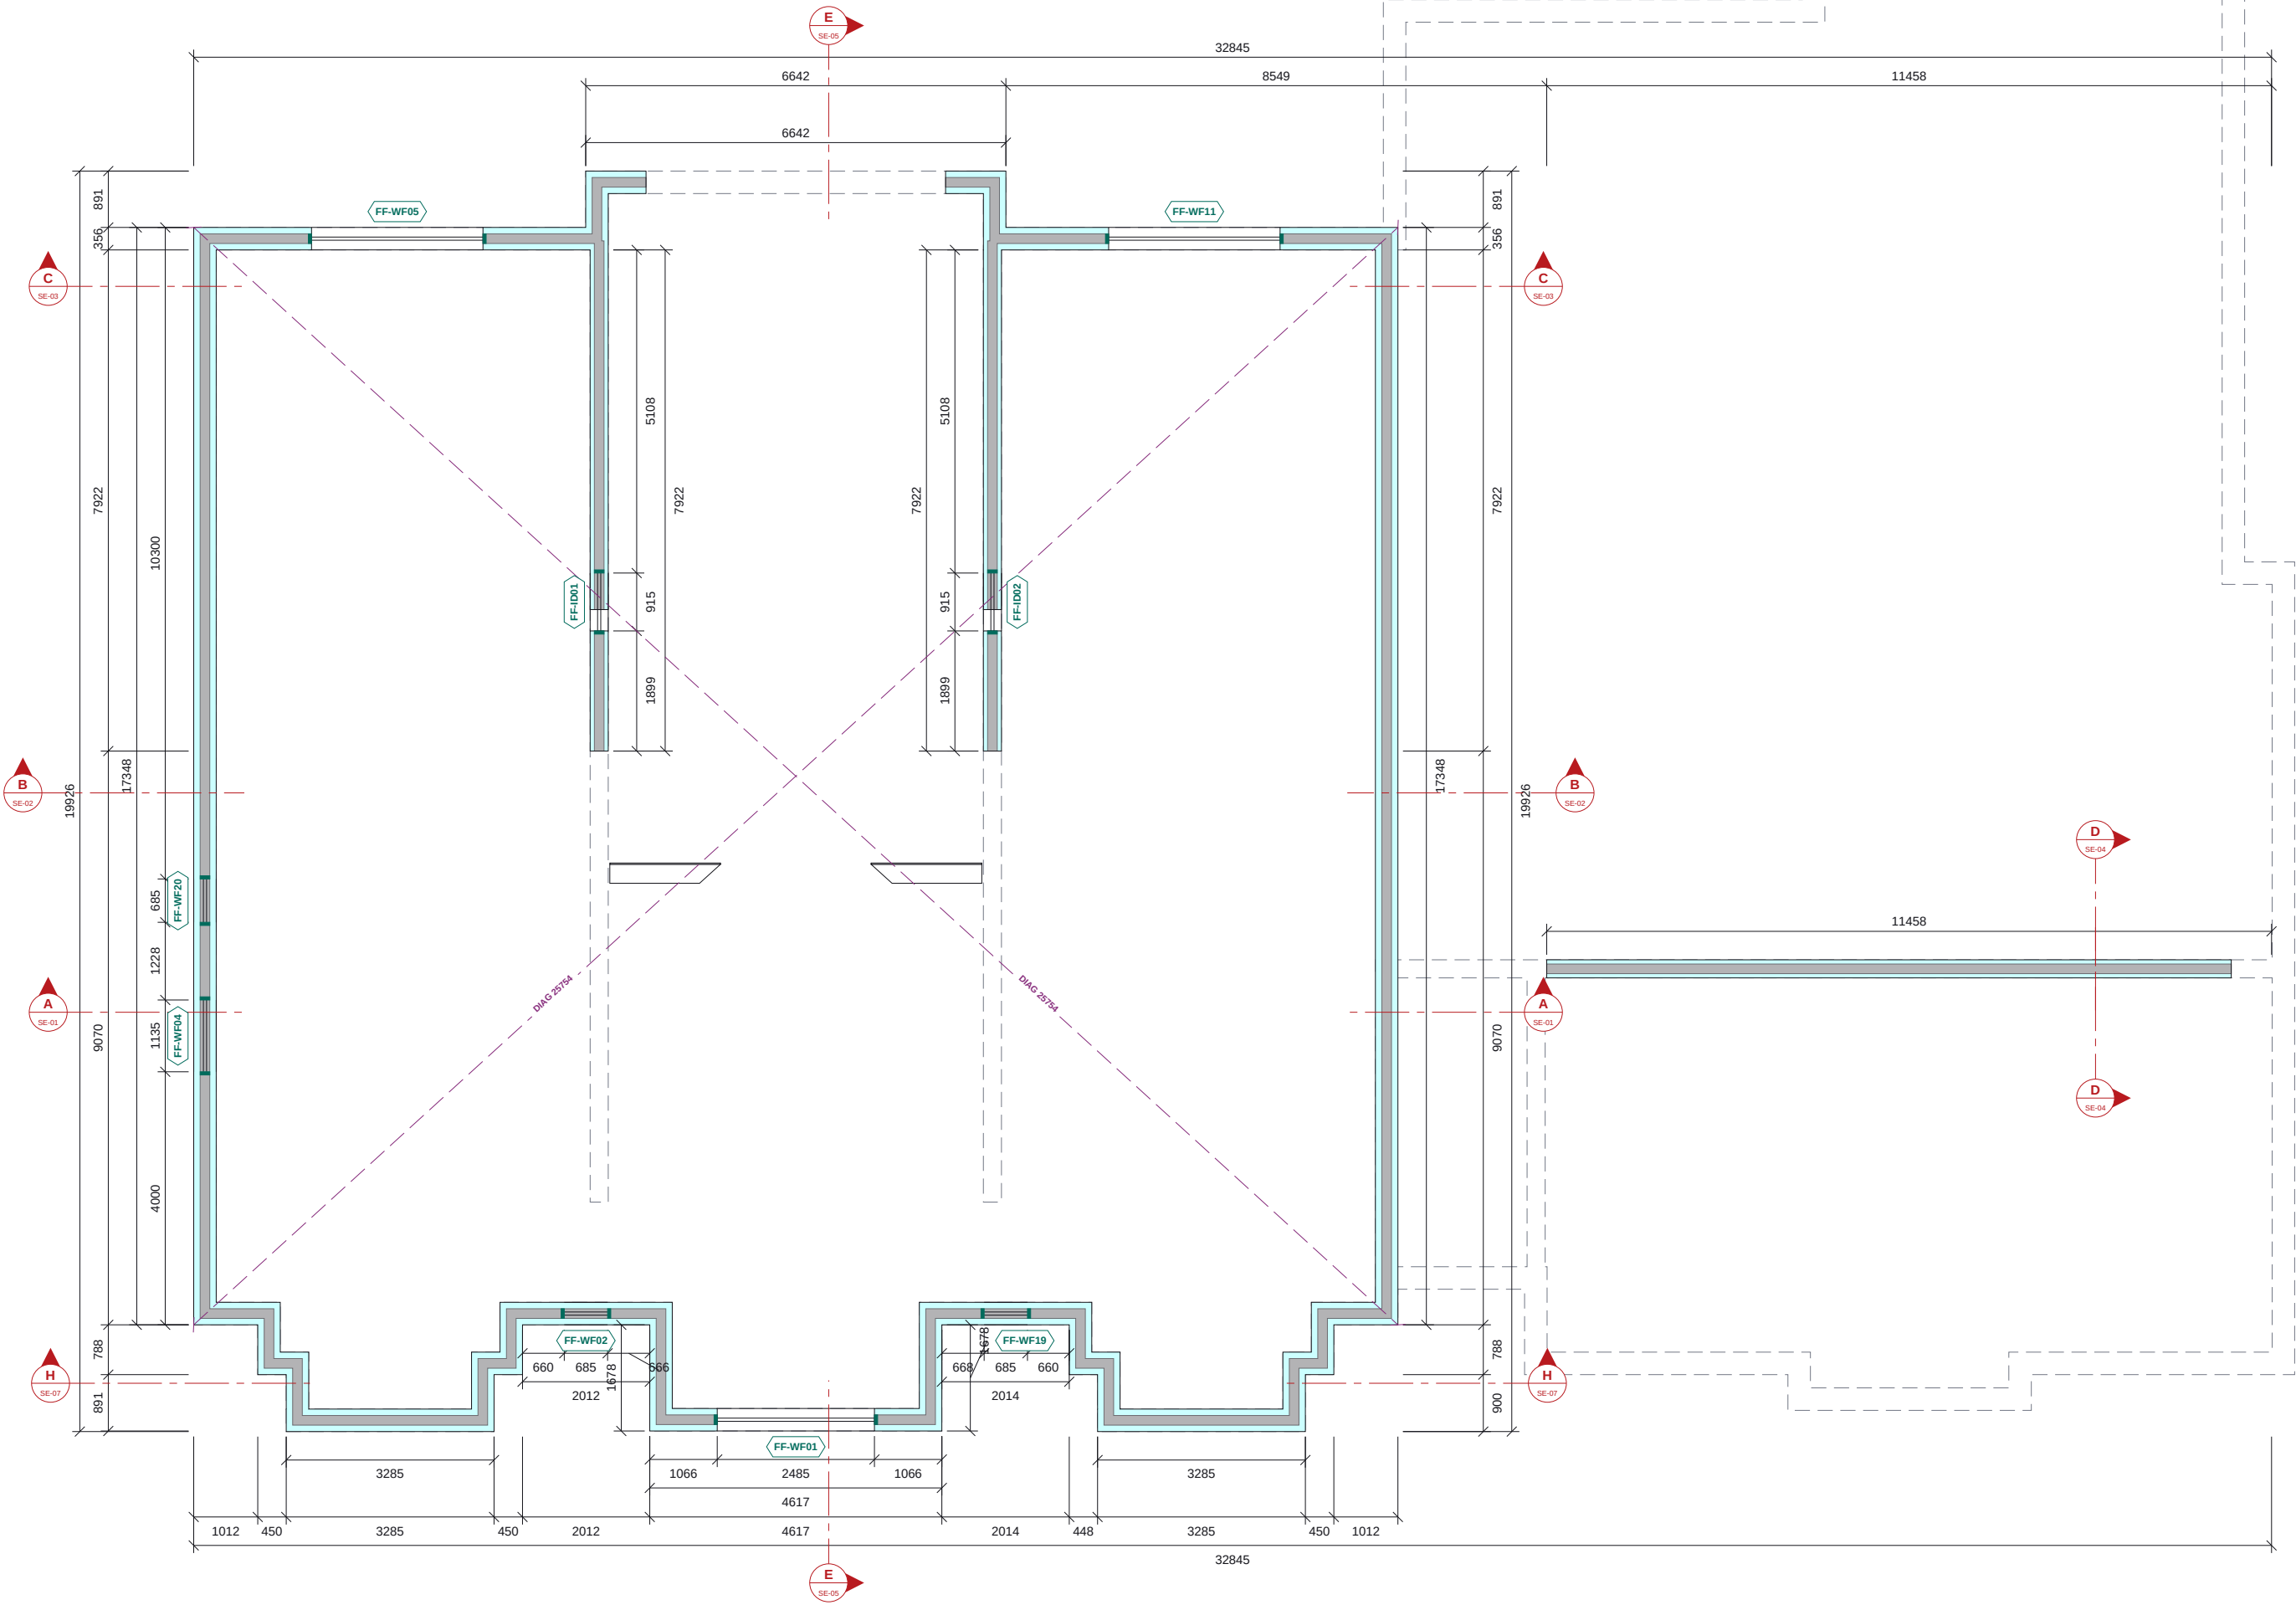

- EPS insulation (Nudura form)
- Concrete core
- End cap at opening
- ICF walls of the level below (dashed)
- Engineer's pier bars (n-H12 vertical bars in ICF pier) / WS wall starters
- Setting-out check diagonal (external ICF corners)
- Section line (see SE sheet)

FF ICF PLAN
Scale 1:100 @ A2 | Plan cut at +4237

NOTES

- ICF: Nudura 6" XR35, 101.6 EPS + 152.4 core + 101.6 EPS = 355.6; 6" Std, 66.7 EPS + 152.4 core + 66.7 EPS = 285.8. Dimensions to the ICF faces.
- Levels above GF FFL (168.748 AOD). Sill / head = structural opening in the ICF.
- ICF per the coordinated model: 6in XR35 (152 mm core, 355.6 mm) external walls, 6in Std (286 mm) internal ICF walls; concrete grade, aggregate, fibre dosage and dowel bars per the Tier Consult specification (to be confirmed).
- Lintel (L-n) and steel (B-n, C-1) marks from Tier Consult 078-TCE-DEN-XX-DR-S-096.210 rev -, which takes precedence. Red EQ tags = queries to the engineer on UKPCS-003-EQ-01 (click to open).
- Masonry walls shown for context.
- Steel over the ICF: see UKPCS-003-GS-02.

REVISIONS

REV	DATE	DESCRIPTION
P01	23.09.26	Approval issue



CLIENT
ICF Homes

PROJECT
Dendrons

DRAWING TITLE
FF ICF GENERAL ARRANGEMENT

ICF walls, openings and setting out

SCALE	SIZE	DATE	DRAWN
1:100	A2	23.09.26	TS

STATUS	DRAWING No.	REV
FOR APPROVAL	UKPCS-003-GA-02	P01