


Do not scale. All dimensions in mm. Check all dimensions on site.

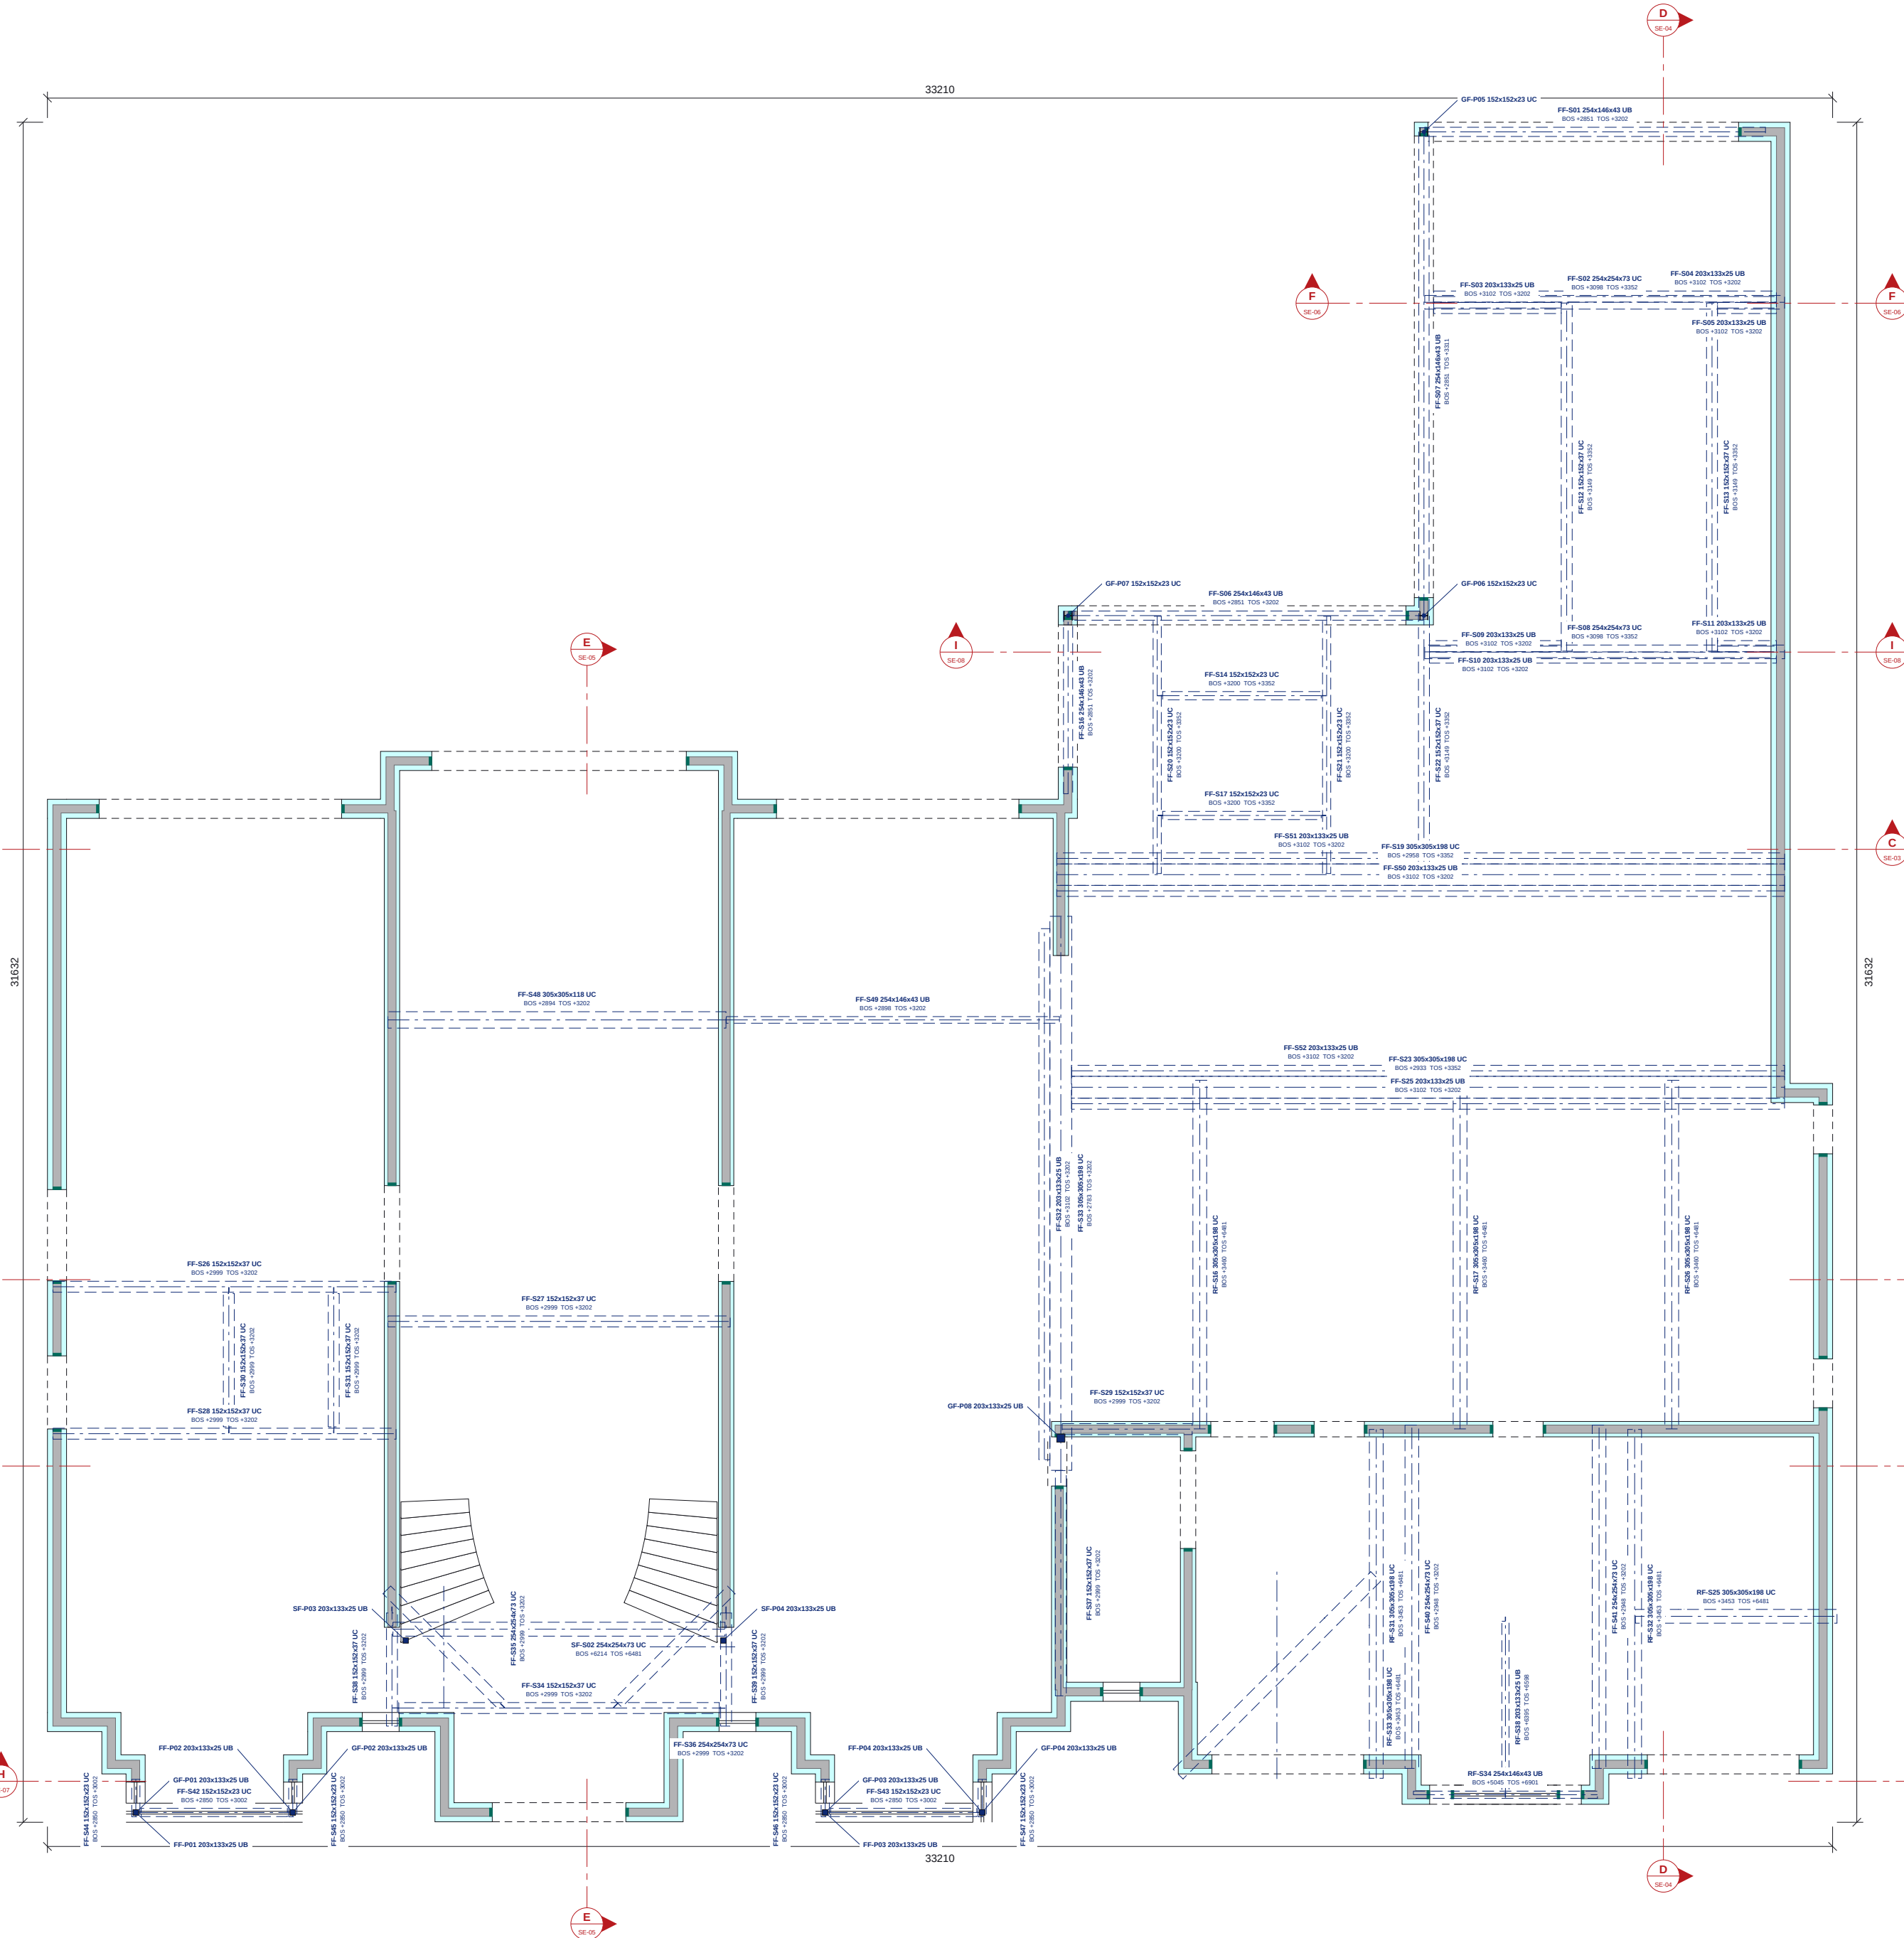

GF STEEL OVER ICF

Scale 1:100 @ A2 | Plan cut at +1382



FOR APPROVAL - NOT FOR CONSTRUCTION

GF STEEL SCHEDULE

STEEL SCHEDULE		BOS	TOS
Mark	Section (engineer)		
FF-S01	254x146x43 UB S355	+2851	+3202
FF-S02	254x254x73 UC S355	+3098	+3352
FF-S03	203x133x25 UB S355	+3102	+3202
FF-S04	203x133x25 UB S355	+3102	+3202
FF-S05	203x133x25 UB S355	+3102	+3202
FF-S06	254x146x43 UB S355	+2851	+3202
FF-S07	254x146x43 UB S355	+2851	+3311
FF-S08	254x254x73 UC S355	+3098	+3352
FF-S09	203x133x25 UB S355	+3102	+3202
FF-S10	203x133x25 UB S355	+3102	+3202
FF-S11	203x133x25 UB S355	+3102	+3202
FF-S12	152x152x37 UC S355	+3149	+3352
FF-S13	152x152x37 UC S355	+3149	+3352
FF-S14	152x152x23 UC S355	+3200	+3352
FF-S16	254x146x43 UB S355	+2851	+3202
FF-S17	152x152x23 UC S355	+3200	+3352
FF-S19	305x305x198 UC S355	+2958	+3352
FF-S20	152x152x23 UC S355	+3200	+3352
FF-S21	152x152x23 UC S355	+3200	+3352
FF-S22	152x152x37 UC S355	+3149	+3352
FF-S23	305x305x198 UC S355	+2933	+3352
FF-S25	203x133x25 UB S355	+3102	+3202
FF-S26	152x152x37 UC S355	+2999	+3202
FF-S27	152x152x37 UC S355	+2999	+3202
FF-S28	152x152x37 UC S355	+2999	+3202
FF-S29	152x152x37 UC S355	+2999	+3202
FF-S30	152x152x37 UC S355	+2999	+3202
FF-S31	152x152x37 UC S355	+2999	+3202
FF-S32	203x133x25 UB S355	+3102	+3202
FF-S33	305x305x198 UC S355	+2783	+3202
FF-S34	152x152x37 UC S355	+2999	+3202
FF-S35	254x254x73 UC S355	+2999	+3202
FF-S36	254x254x73 UC S355	+2999	+3202
FF-S37	152x152x37 UC S355	+2999	+3202
FF-S38	152x152x37 UC S355	+2999	+3202
FF-S39	152x152x37 UC S355	+2999	+3202
FF-S40	254x254x73 UC S355	+2948	+3202
FF-S41	254x254x73 UC S355	+2948	+3202
FF-S42	152x152x23 UC S355	+2850	+3002
FF-S43	152x152x23 UC S355	+2850	+3002
FF-S44	152x152x23 UC S355	+2850	+3002
FF-S45	152x152x23 UC S355	+2850	+3002
FF-S46	152x152x23 UC S355	+2850	+3002
FF-S47	152x152x23 UC S355	+2850	+3002
FF-S48	305x305x118 UC S355	+2894	+3202
FF-S49	254x146x43 UB S355	+2898	+3202
FF-S50	203x133x25 UB S355	+3102	+3202
FF-S51	203x133x25 UB S355	+3102	+3202
FF-S52	203x133x25 UB S355	+3102	+3202
RF-S16	305x305x198 UC S355	+3460	+6481
RF-S17	305x305x198 UC S355	+3460	+6481
RF-S25	305x305x198 UC S355	+3453	+6481
RF-S26	305x305x198 UC S355	+3460	+6481
RF-S31	305x305x198 UC S355	+3453	+6481
RF-S32	305x305x198 UC S355	+3453	+6481
RF-S33	305x305x198 UC S355	+3453	+6481
RF-S34	254x146x43 UB S355	+5045	+6901
RF-S38	203x133x25 UB S355	+6395	+6996
SF-S02	254x254x73 UC S355	+6214	+6481
FF-P01	203x133x25 UB S355	+3352	+5925
FF-P02	203x133x25 UB S355	+3352	+5925
FF-P03	203x133x25 UB S355	+3352	+5925
FF-P04	203x133x25 UB S355	+3352	+5925
GF-P01	203x133x25 UB S355	-98	+2850
GF-P02	203x133x25 UB S355	-98	+2850
GF-P03	203x133x25 UB S355	-98	+2850
GF-P04	203x133x25 UB S355	-98	+2850
GF-P05	152x152x23 UC S355	-98	+2851
GF-P06	152x152x23 UC S355	-98	+2851
GF-P07	152x152x23 UC S355	-98	+2851
GF-P08	203x133x25 UB S355	-98	+2783
SF-P03	203x133x25 UB S355	+6481	+7559
SF-P04	203x133x25 UB S355	+6481	+7559

BOS / TOS = bottom / top of steel above GF FFL (C-1 columns: base / top).

NOTES

- ICF per the coordinated model: 6in XR35 (152 mm core, 355.6 mm) external walls, 6in Std (286 mm) internal ICF walls; concrete grade, aggregate, fibre dosage and dowel length per the Tier Consult specification (to be confirmed).
- Lintel (L-n) and Steel (B-n, C-1) marks from Tier Consult 078-TCE-DEN-XX-DR-S-096.210 rev -, which takes precedence. Red EQ tags = queries to the engineer on UKPCS-003-EQ-01 (click to open).
- Masonry walls shown for context.
- Steel over dashed. BOS / TOS = bottom / top of steel above GF FFL.
- Steel over the ICF at this level, dashed, with the engineer's member marks as modelled; BOS / TOS = bottom / top of steel above GF FFL. Columns cut at the plan level shown solid.
- Walls and openings: see UKPCS-003-GA-01 for the ICF setting out, opening sizes and the opening schedule.
- No structural grid is registered on this issue.

REVISIONS

REV	DATE	DESCRIPTION
P01	23.09.26	Approval issue



CLIENT
ICF Homes

PROJECT
Dendrons

DRAWING TITLE

GF STEEL OVER ICF

Steel over the ICF, marked and scheduled

SCALE 1:100	SIZE A2	DATE 23.09.26	DRAWN TS
----------------	------------	------------------	-------------

STATUS	DRAWING No.	
	UKPCS-003-GS-01	
FOR APPROVAL		

P01