

FOR APPROVAL - NOT FOR CONSTRUCTION

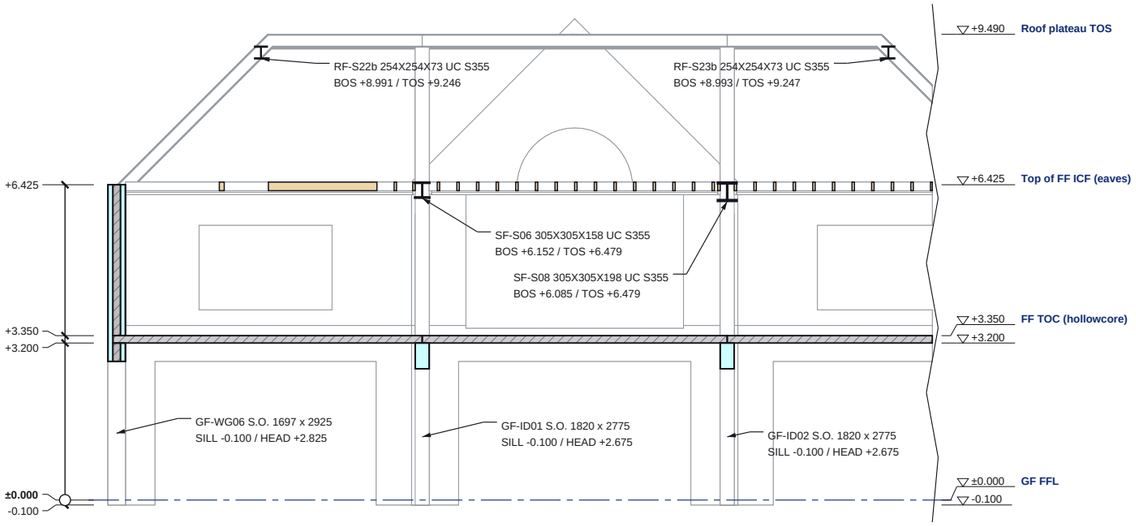


## SECTION B-B (PART 1 OF 2)

Scale 1:125 @ A3 | Looking north; levels above GF FFL

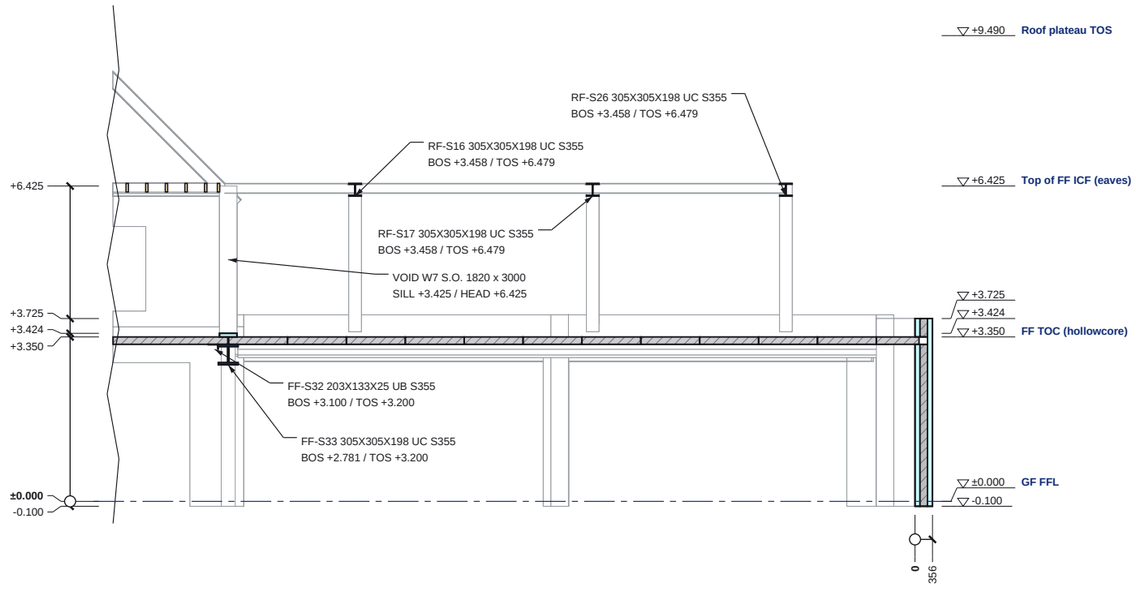


## SECTION B-B (PART 2 OF 2)

Scale 1:125 @ A3 | Looking north; levels above GF FFL

ICF EPS (cut)
ICF concrete core / RC (cut)
Steel (cut)
Beyond the cut (line work)

0 1 2 3 4 5m

Do not scale. All dimensions in millimetres; levels in metres from GF FFL. Check all dimensions on site.

## SECTION B-B SCHEDULES


### LEVELS ON THIS SECTION

| Level | FFL | AOD |
|---|---|---|
| underside of ICF | -0.100 | 168.648 |
| GF FFL | ±0.000 | 168.748 |
| top of ICF W43 | +3.200 | 171.948 |
| FF TOC (hollowcore) | +3.350 | 172.098 |
| top of ICF W07 | +3.424 | 172.172 |
| top of ICF W13 | +3.725 | 172.473 |
| Top of FF ICF (eaves) | +6.425 | 175.173 |
| Roof plateau TOS | +9.490 | 178.238 |

### STEEL CUT BY THIS SECTION

| Mark | Section (engineer) | BOS | TOS |
|---|---|---|---|
| FF-S32 | 203x133x25 UB S355 | +3.100 | +3.200 |
| FF-S33 | 305x305x198 UC S355 | +2.781 | +3.200 |
| RF-S16 | 305x305x198 UC S355 | +3.458 | +6.479 |
| RF-S17 | 305x305x198 UC S355 | +3.458 | +6.479 |
| RF-S26 | 305x305x198 UC S355 | +3.458 | +6.479 |
| RF-S22b | 254x254x73 UC S355 | +8.991 | +9.246 |
| RF-S23b | 254x254x73 UC S355 | +8.993 | +9.247 |
| SF-S06 | 305x305x158 UC S355 | +6.152 | +6.479 |
| SF-S08 | 305x305x198 UC S355 | +6.085 | +6.479 |

### SECTION KEY

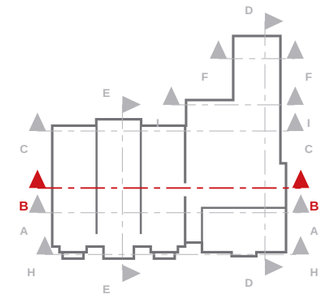


### NOTES

1. Section B-B is a BuildEase ICF section (not an architect's section line). Cut elements hatched / filled; the model beyond the cut in line work.
2. Levels above GF FFL (168.748 AOD); the level table gives AOD.
3. ICF: Nudura 6" XR35, 101.6 EPS + 152.4 core + 101.6 EPS = 355.6; 6" Std, 66.7 EPS + 152.4 core + 66.7 EPS = 285.8, 152.4 core + 101.6 EPS = 355.6. ICF per the coordinated model: 6in XR35 (152 mm core, 355.6 mm) external walls, 6in Std (286 mm) internal ICF walls; concrete grade, aggregate, fibre dosage and dowel bars per the Tier Consult specification (to be confirmed).
4. Steel marks, BOS / TOS: Tier Consult 078-TCE-DEN-XX-DR-S-096..210 rev -. See UKPCS-003-GA-01 / EL-01 / EL-02 in the approval drawings pack.

### REVISIONS

| REV | DATE | DESCRIPTION |
|---|---|---|
| P01 | 23.09.26 | Approval issue |
| P02 | 15.10.26 | Revised to the P01 comments |

Nudura™ BuildEase

| CLIENT | PROJECT |
|---|---|
| ICF Homes | Dendrons |

DRAWING TITLE
**SECTION B-B**
ICF section with levels and build-ups

| SCALE | SIZE | DATE |
|---|---|---|
| 1:125 | A3 | 15.10.26 |
| DRAWN | CHECKED | APPROVED |
| TS | | |

| STATUS | DRAWING No. | REV |
|---|---|---|
| FOR APPROVAL | UKPCS-003-SE-02 | P02 |