
FOR APPROVAL - NOT FOR CONSTRUCTION

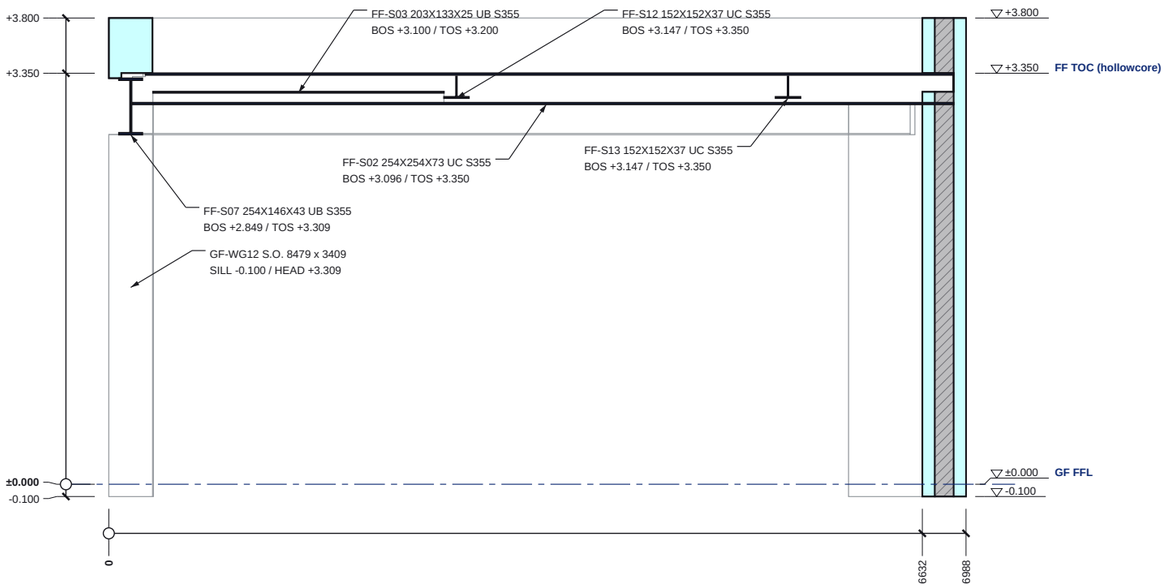


## SECTION F-F

Scale 1:50 @ A3 | Looking north; levels above GF FFL

ICF EPS (cut)
ICF concrete core / RC (cut)
Steel (cut)
Beyond the cut (line work)

0 1 2m

Do not scale. All dimensions in millimetres, levels in metres from GF FFL. Check all dimensions on site.

## SECTION F-F SCHEDULES


### LEVELS ON THIS SECTION

| Level | FFL | AOD |
|---|---|---|
| underside of ICF | -0.100 | 168.648 |
| GF FFL | ±0.000 | 168.748 |
| FF TOC (hollowcore) | +3.350 | 172.098 |
| top of ICF W11 | +3.800 | 172.548 |

### STEEL CUT BY THIS SECTION

| Mark | Section (engineer) | BOS | TOS |
|---|---|---|---|
| FF-S02 | 254x254x73 UC S355 | +3.096 | +3.350 |
| FF-S03 | 203x133x25 UB S355 | +3.100 | +3.200 |
| FF-S07 | 254x146x43 UB S355 | +2.849 | +3.309 |
| FF-S12 | 152x152x37 UC S355 | +3.147 | +3.350 |
| FF-S13 | 152x152x37 UC S355 | +3.147 | +3.350 |

### SECTION KEY

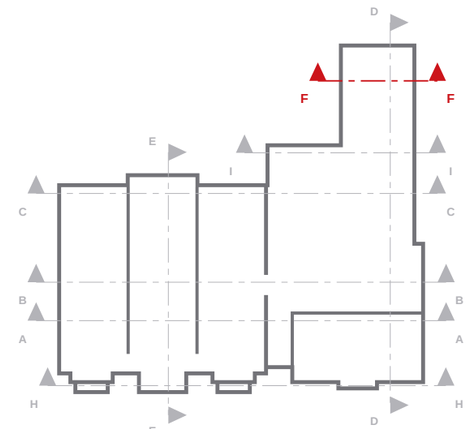


### NOTES

1. Section F-F is a BuildEase ICF section (not an architect's section line). Cut elements hatched / filled; the model beyond the cut in line work.
2. Levels above GF FFL (168.748 AOD); the level table gives AOD.
3. ICF: Nudura 6" XR35, 101.6 EPS + 152.4 core + 101.6 EPS = 355.6; 6" Std, 66.7 EPS + 152.4 core + 66.7 EPS = 285.8, 152.4 core + 101.6 EPS = 355.6. ICF per the coordinated model: 6in XR35 (152 mm core, 355.6 mm) external walls, 6in Std (286 mm) internal ICF walls; concrete grade, aggregate, fibre dosage and dowel bars per the Tier Consult specification (to be confirmed).
4. Steel marks, BOS / TOS: Tier Consult 078-TCE-DEN-XX-DR-S-096..210 rev -. See UKPCS-003-GA-01 / EL-01 / EL-02 in the approval drawings pack.

### REVISIONS

| REV | DATE | DESCRIPTION |
|---|---|---|
| P01 | 23.09.26 | Approval issue |
| P02 | 15.10.26 | Revised to the P01 comments |

Nudura™ BuildEase

| CLIENT | PROJECT |
|---|---|
| ICF Homes | Dendrons |

DRAWING TITLE
**SECTION F-F**

ICF section with levels and build-ups

| SCALE | SIZE | DATE |
|---|---|---|
| 1:50 | A3 | 15.10.26 |
| DRAWN | CHECKED | APPROVED |
| TS | | |

| STATUS | DRAWING No. | REV |
|---|---|---|
| FOR APPROVAL | UKPCS-003-SE-06 | P02 |