


Do not scale. All dimensions in mm. Check all dimensions on site.



FOR APPROVAL - NOT FOR CONSTRUCTION

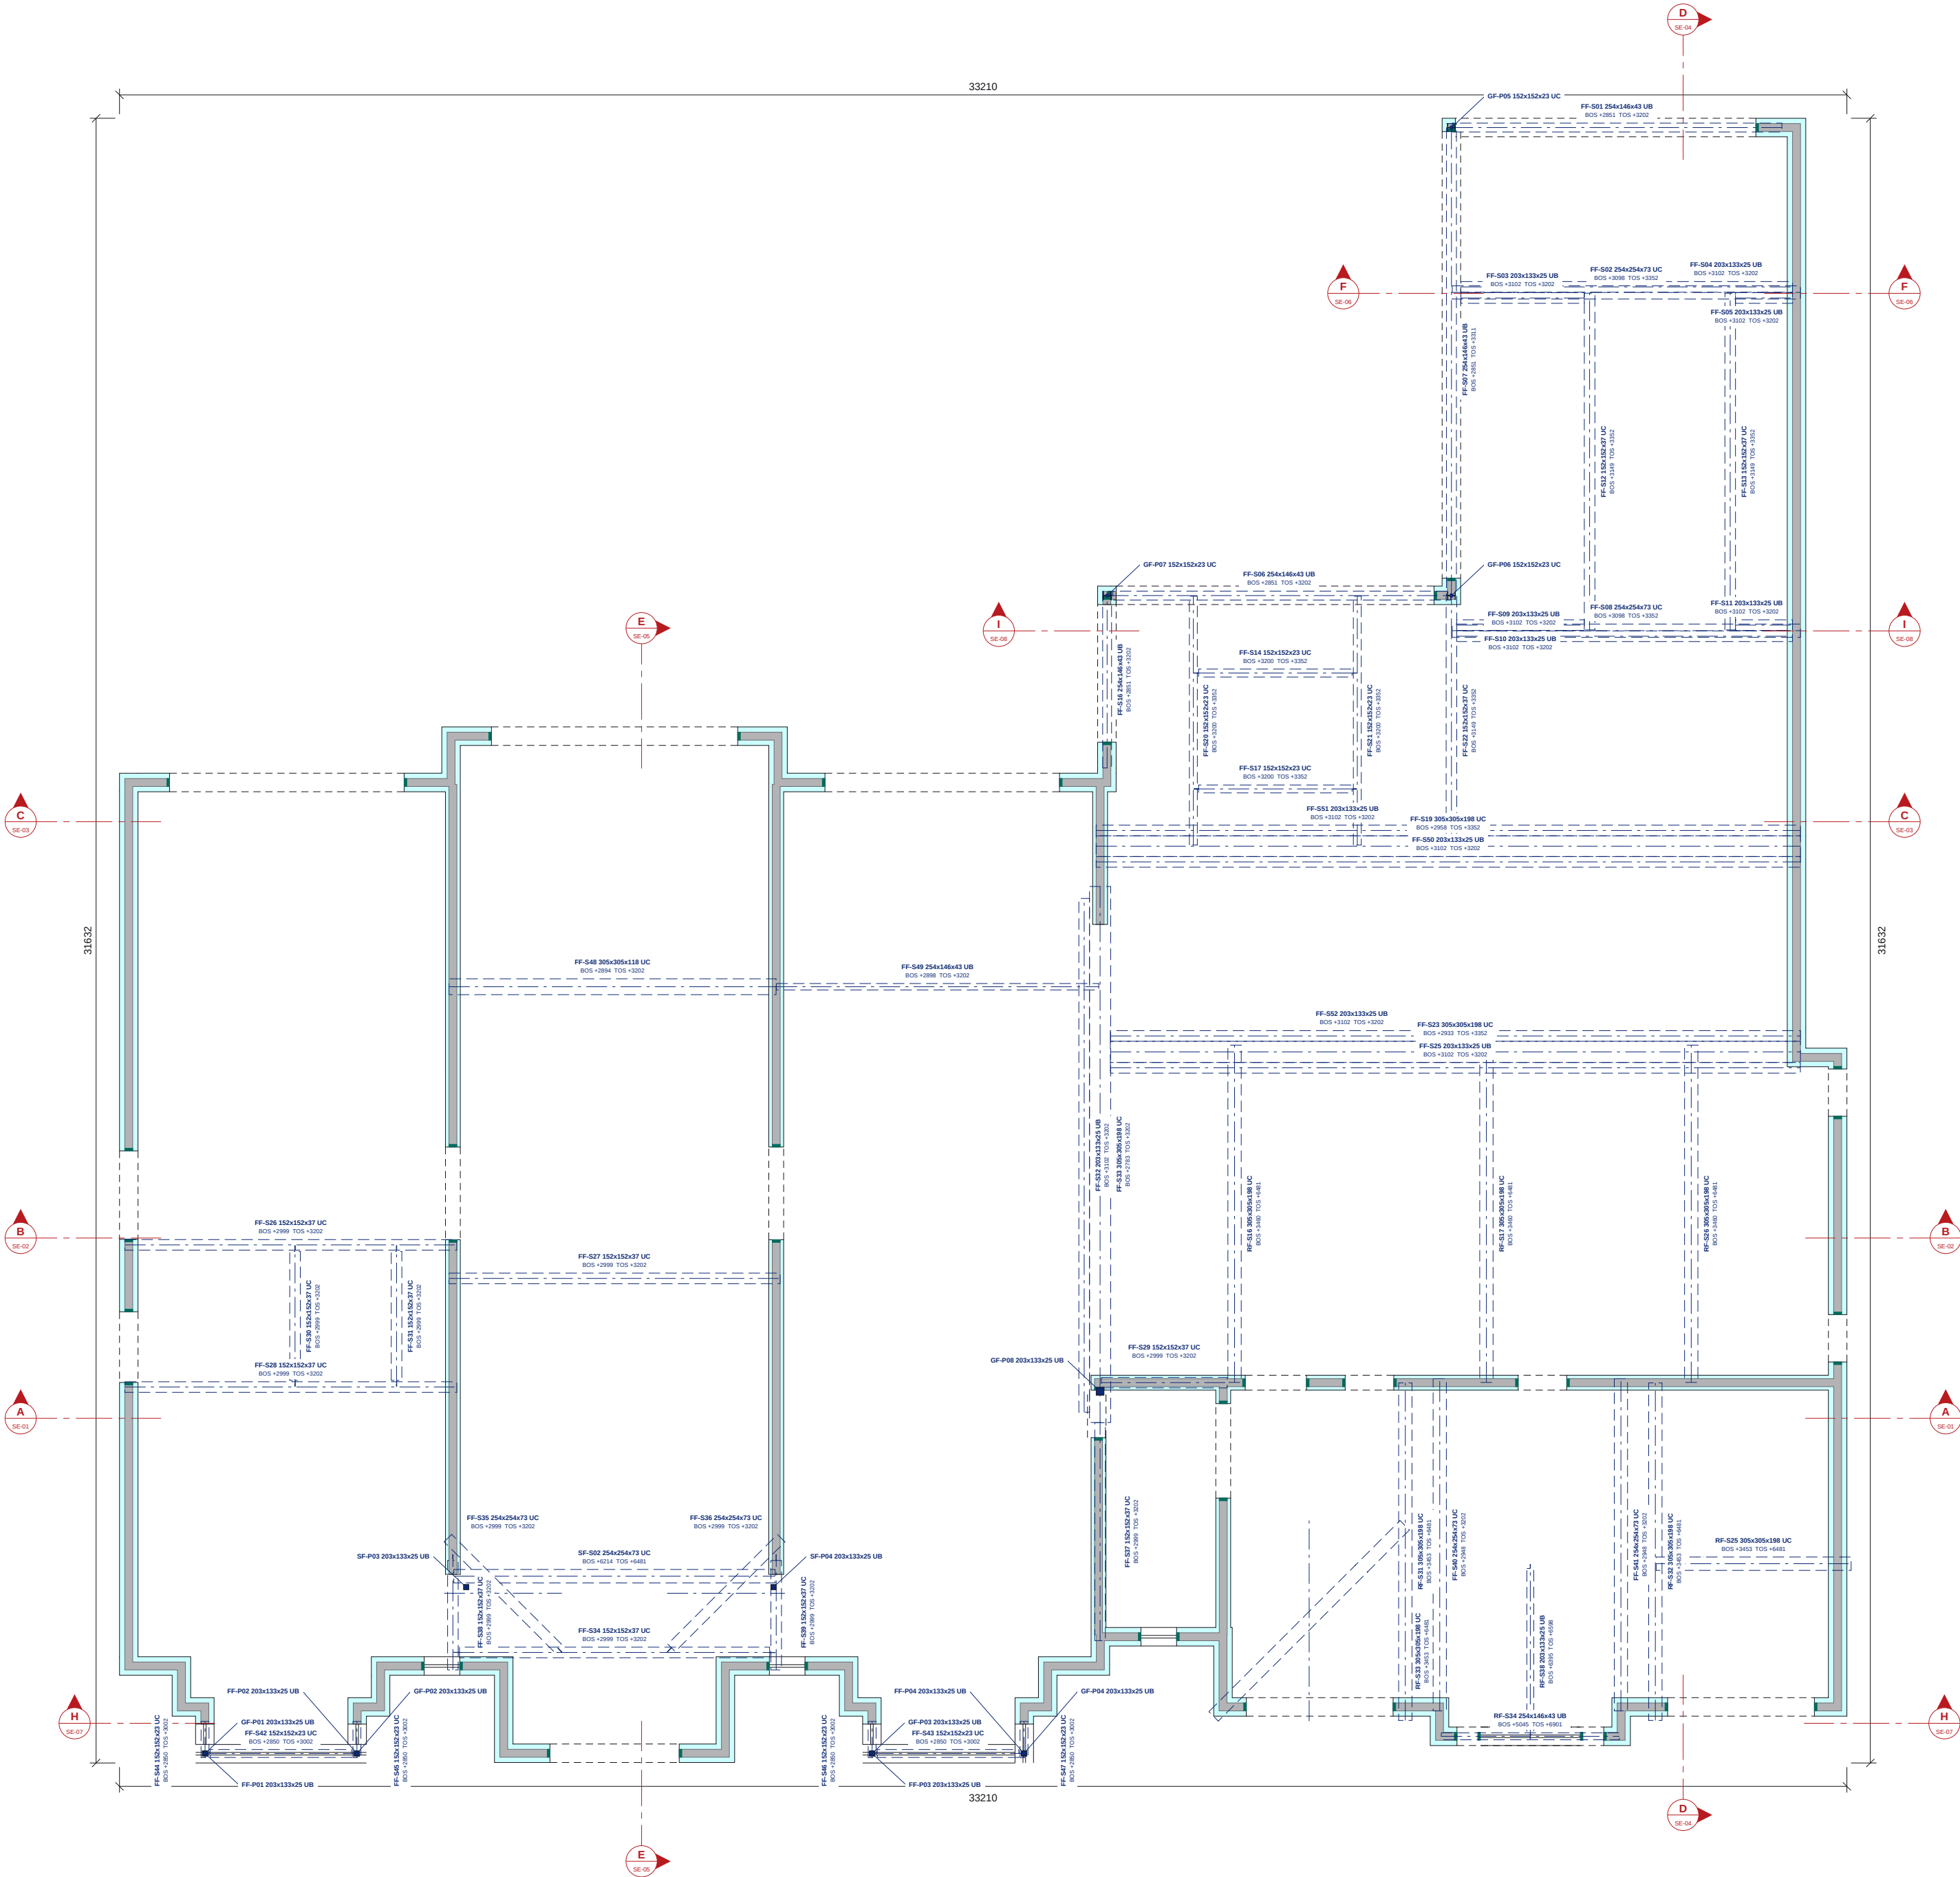

GF STEEL OVER ICF
Scale 1:100 @ A2 | Plan cut at +1382

GF STEEL SCHEDULE

STEEL SCHEDULE		BOS	TOS
Mark	Section (engineer)		
FF-S01	254x146x43 UB S355	+2851	+3202
FF-S02	254x254x73 UC S355	+3098	+3352
FF-S03	203x133x25 UB S355	+3102	+3202
FF-S04	203x133x25 UB S355	+3102	+3202
FF-S05	203x133x25 UB S355	+3102	+3202
FF-S06	254x146x43 UB S355	+2851	+3202
FF-S07	254x146x43 UB S355	+2851	+3311
FF-S08	254x254x73 UC S355	+3098	+3352
FF-S09	203x133x25 UB S355	+3102	+3202
FF-S10	203x133x25 UB S355	+3102	+3202
FF-S11	203x133x25 UB S355	+3102	+3202
FF-S12	152x152x37 UC S355	+3149	+3352
FF-S13	152x152x37 UC S355	+3149	+3352
FF-S14	152x152x23 UC S355	+3200	+3352
FF-S16	254x146x43 UB S355	+2851	+3202
FF-S17	152x152x23 UC S355	+3200	+3352
FF-S19	305x305x198 UC S355	+2958	+3352
FF-S20	152x152x23 UC S355	+3200	+3352
FF-S21	152x152x23 UC S355	+3200	+3352
FF-S22	152x152x37 UC S355	+3149	+3352
FF-S23	305x305x198 UC S355	+2933	+3352
FF-S25	203x133x25 UB S355	+3102	+3202
FF-S26	152x152x37 UC S355	+2999	+3202
FF-S27	152x152x37 UC S355	+2999	+3202
FF-S28	152x152x37 UC S355	+2999	+3202
FF-S29	152x152x37 UC S355	+2999	+3202
FF-S30	152x152x37 UC S355	+2999	+3202
FF-S31	152x152x37 UC S355	+2999	+3202
FF-S32	203x133x25 UB S355	+3102	+3202
FF-S33	305x305x198 UC S355	+2783	+3202
FF-S34	152x152x37 UC S355	+2999	+3202
FF-S35	254x254x73 UC S355	+2999	+3202
FF-S36	254x254x73 UC S355	+2999	+3202
FF-S37	152x152x37 UC S355	+2999	+3202
FF-S38	152x152x37 UC S355	+2999	+3202
FF-S39	152x152x37 UC S355	+2999	+3202
FF-S40	254x254x73 UC S355	+2948	+3202
FF-S41	254x254x73 UC S355	+2948	+3202
FF-S42	152x152x23 UC S355	+2850	+3002
FF-S43	152x152x23 UC S355	+2850	+3002
FF-S44	152x152x23 UC S355	+2850	+3002
FF-S45	152x152x23 UC S355	+2850	+3002
FF-S46	152x152x23 UC S355	+2850	+3002
FF-S47	152x152x23 UC S355	+2850	+3002
FF-S48	305x305x118 UC S355	+2894	+3202
FF-S49	254x146x43 UB S355	+2898	+3202
FF-S50	203x133x25 UB S355	+3102	+3202
FF-S51	203x133x25 UB S355	+3102	+3202
FF-S52	203x133x25 UB S355	+3102	+3202
RF-S16	305x305x198 UC S355	+3460	+6481
RF-S17	305x305x198 UC S355	+3460	+6481
RF-S25	305x305x198 UC S355	+3453	+6481
RF-S26	305x305x198 UC S355	+3460	+6481
RF-S31	305x305x198 UC S355	+3453	+6481
RF-S32	305x305x198 UC S355	+3453	+6481
RF-S33	305x305x198 UC S355	+3453	+6481
RF-S34	254x146x43 UB S355	+5045	+6901
RF-S38	203x133x25 UB S355	+4035	+6996
SF-S02	254x254x73 UC S355	+6214	+6481
FF-P01	203x133x25 UB S355	+3352	+5925
FF-P02	203x133x25 UB S355	+3352	+5925
FF-P03	203x133x25 UB S355	+3352	+5925
FF-P04	203x133x25 UB S355	+3352	+5925
GF-P01	203x133x25 UB S355	-98	+2850
GF-P02	203x133x25 UB S355	-98	+2850
GF-P03	203x133x25 UB S355	-98	+2850
GF-P04	203x133x25 UB S355	-98	+2850
GF-P05	152x152x23 UC S355	-98	+2851
GF-P06	152x152x23 UC S355	-98	+2851
GF-P07	152x152x23 UC S355	-98	+2851
GF-P08	203x133x25 UB S355	-98	+2783
SF-P03	203x133x25 UB S355	+6481	+7559
SF-P04	203x133x25 UB S355	+6481	+7559

BOS / TOS = bottom / top of steel above GF FFL (C-1 columns: base / top).

NOTES

- ICF per the coordinated model: 6in XR35 (152 mm core, 355.6 mm) external walls, 6in Std (286 mm) internal ICF walls; concrete grade, aggregate, fibre dosage and dowel bars per the Tier Consult specification (to be confirmed).
- Lintel (L-n) and steel (B-n, C-1) marks from Tier Consult 078-TCE-DEN-XX-DR-S-096.210 rev -, which takes precedence. Red EQ tags = queries to the engineer on UKPCS-003-EQ-01 (click to open).
- Masonry walls shown for context.
- Steel over dashed. BOS / TOS = bottom / top of steel above GF FFL.
- Steel over the ICF at this level, dashed, with the engineer's member marks as modelled; BOS / TOS = bottom / top of steel above GF FFL. Columns cut at the plan level shown solid.
- Walls and openings: see UKPCS-003-GA-01 for the ICF setting out, opening sizes and the opening schedule.
- No structural grid is registered on this issue.

REVISIONS

REV	DATE	DESCRIPTION
P01	23.09.26	Approval issue



CLIENT ICF Homes	PROJECT Dendrons
---------------------	---------------------

DRAWING TITLE
GF STEEL OVER ICF

Steel over the ICF, marked and scheduled

SCALE 1:100	SIZE A2	DATE 23.09.26	DRAWN TS
----------------	------------	------------------	-------------

STATUS	DRAWING No.		REV
FOR APPROVAL			

P01