



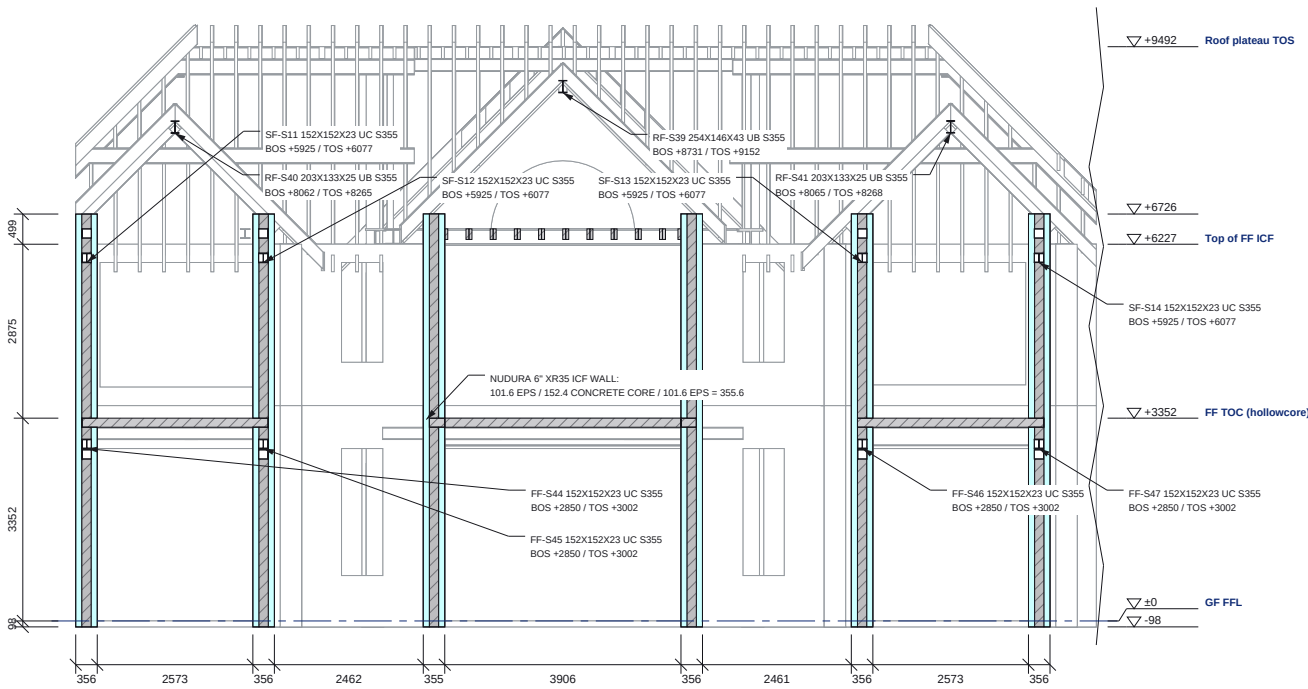

SECTION H-H (PART 1 OF 2)

Scale 1:125 @ A3 | Looking north; levels above GF FFL

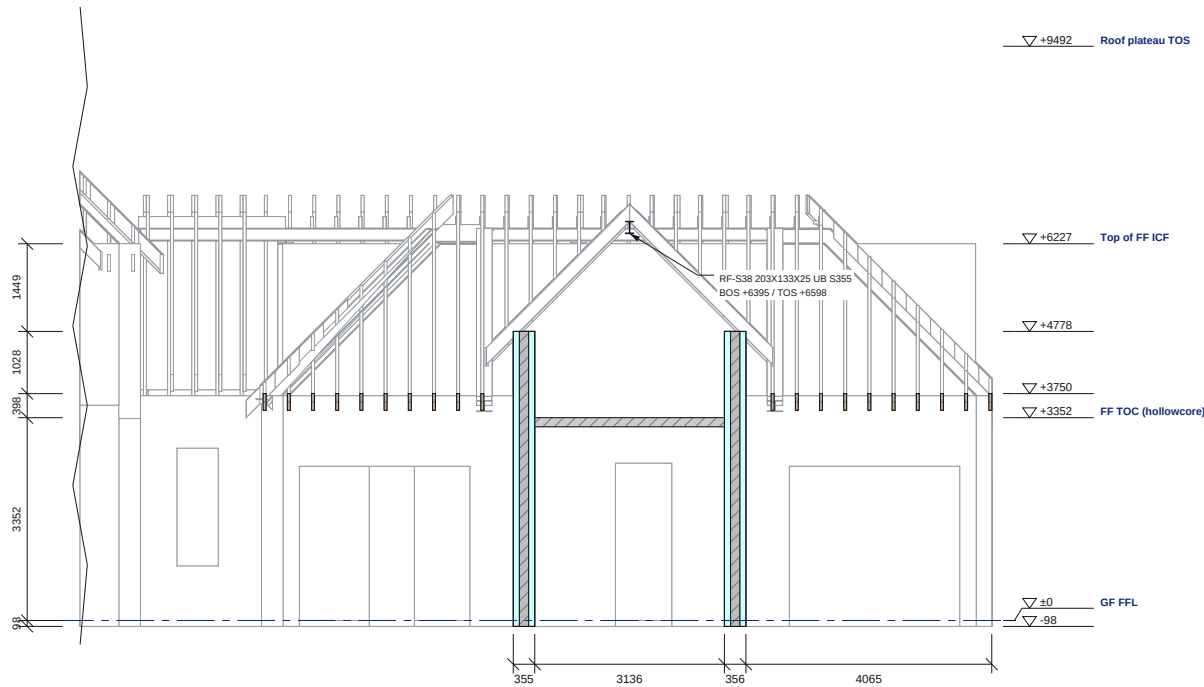

SECTION H-H (PART 2 OF 2)

Scale 1:125 @ A3 | Looking north; levels above GF FFL

- ICF EPS (cut)

ICF concrete core / RC (cut)

Steel (cut)

Screed
- Insulation (PIR / XPS, perimeter)

Blinding / hardcore

Beyond the cut (line work)



SECTION H-H SCHEDULES


LEVELS ON THIS SECTION

Level	FFL	AOD
underside of ICF	-98	168.650
GF FFL	0	168.748
FF TOC (hollowcore)	+3352	172.100
top of roof build-up	+3750	172.498
top of ICF	+4778	173.526
Top of FF ICF	+6227	174.975
top of ICF	+6726	175.474
Roof plateau TOS	+9492	178.240

STEEL CUT BY THIS SECTION

Mark	Section (engineer)	BOS	TOS
FF-S44	152x152x23 UC S355	+2850	+3002
FF-S45	152x152x23 UC S355	+2850	+3002
FF-S46	152x152x23 UC S355	+2850	+3002
FF-S47	152x152x23 UC S355	+2850	+3002
RF-S38	203x133x25 UB S355	+6395	+6598
RF-S39	254x146x43 UB S355	+8731	+9152
RF-S40	203x133x25 UB S355	+8062	+8265
RF-S41	203x133x25 UB S355	+8065	+8268
SF-S11	152x152x23 UC S355	+5925	+6077
SF-S12	152x152x23 UC S355	+5925	+6077
SF-S13	152x152x23 UC S355	+5925	+6077
SF-S14	152x152x23 UC S355	+5925	+6077

SECTION KEY

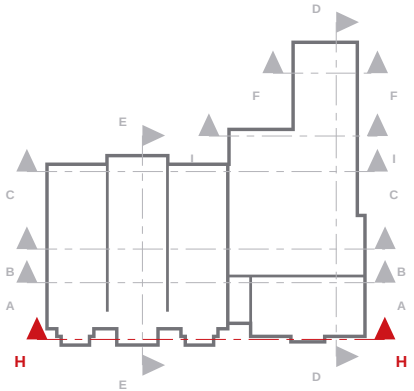

NOTES

- Section H-H is a BuildEase ICF section (not an architect's section line). Cut elements hatched / filled; the model beyond the cut in line work.
- Levels above GF FFL (168.748 AOD); the level table gives AOD.
- ICF: Nudura 6" XR35, 101.6 EPS + 152.4 core + 101.6 EPS = 355.6; 6" Std, 66.7 EPS + 152.4 core + 66.7 EPS = 285.8, 152.4 core + 101.6 EPS = 355.6. ICF per the coordinated model: 6in XR35 (152 mm core, 355.6 mm) external walls, 6in Std (286 mm) internal ICF walls; concrete grade, aggregate, fibre dosage and dowel bars per the Tier Consult specification (to be confirmed).
- Steel marks, BOS / TOS: Tier Consult 078-TCE-DEN-XX-DR-S-096..210 rev -. See UKPCS-003-GA-01 / EL-01 / EL-02.

REVISIONS

REV	DATE	DESCRIPTION
P01	23.09.26	Approval issue



CLIENT

ICF Homes

PROJECT

Dendrons

DRAWING TITLE

SECTION H-H

ICF section with levels and build-ups

SCALE	SIZE	DATE	DRAWN
1:125	A3	23.09.26	TS

STATUS	DRAWING No.	REV
FOR APPROVAL	UKPCS-003-SE-07	P01